

Golden Rock Stone AI - Preliminary Shop Drawing Result

Based on: Cladding Shop drawings 17.pdf | Drawing 17 | Palm Jumeirah

RESULT STATUS: PRELIMINARY - NOT FOR FABRICATION

Selected interpretation from the supplied details

- External wall stone cladding with U-Channel 41x41x41 mm option
- Project Option 2 profile: 25 mm stone, 5 mm horizontal joint, 2 mm vertical joint
- Parapet groove: 20 mm width x 5 or 10 mm depth (confirm from approved detail)
- Corner: 5 mm machine cut; 45 degree mitre or 5 mm then 45 degree Bird's Mouth
- Groove detail: 10 x 10 mm, glue to approved mockup
- Typical details: elevation, window side, wall corner, typical crown, roof/balustrade crown

The source drawing is retained after this summary for visual coordination.

Applied system rules

U-Channel quantity basis: 4 large brackets 100x100 mm per channel piece (2 top + 2 bottom) and 4 small reverse brackets 50x100 mm between them. Pin diameter 5 mm with 20 mm embedment. Rock Wool 50 mm is optional. Cementitious waterproofing is 2 coats x 2 mm (4 mm total), using MasterSeal 550, Sika, or approved equivalent. Panel height limit is 700 mm. Minimum panel width remains project/material dependent and is not fixed.

Detail Register and Coordination Schedule

Detail 72

Window / head / sill fixing detail

Confirm written fixing dimensions and waterproofing returns.

Detail 73

Wall / window side section

Coordinate U-channel, Rock Wool, cavity and final stone face.

Detail 74

Crown / FFL adjustment detail

Source note: FFL increased by 60 mm; verify revised level.

Detail 75

External corner / return detail

Select 45 degree mitre or Bird's Mouth option.

Detail 76

Typical wall / parapet elevation

Apply 700 mm maximum panel height and equalized layout.

Detail 77


Parapet / crown edge detail

All horizontal stone edges to slope slightly for drainage.

RFI Register - Required Before Fabrication

1. Verified wall width/height, slab sizes, kerf and edge trim are not provided in the drawing set.
2. Confirm U-channel piece count and approved bracket projection for each zone.
3. Confirm anchor/hole/fixing dimensions, corner returns and stone pin arrangement.
4. Confirm cavity reference (waterproofing face or insulation face), Rock Wool selection and final stone face.
5. Confirm whether parapet groove depth is 5 mm or 10 mm and approve the 10x10 mm groove/mockup glue detail.
6. Coordinate drawing dimensions and levels with site survey before production.

CLADDING LEGEND (STONE & MARBLE)		
SYMBOL	DESCRIPTION	MATERIAL
	Crown	Travertine

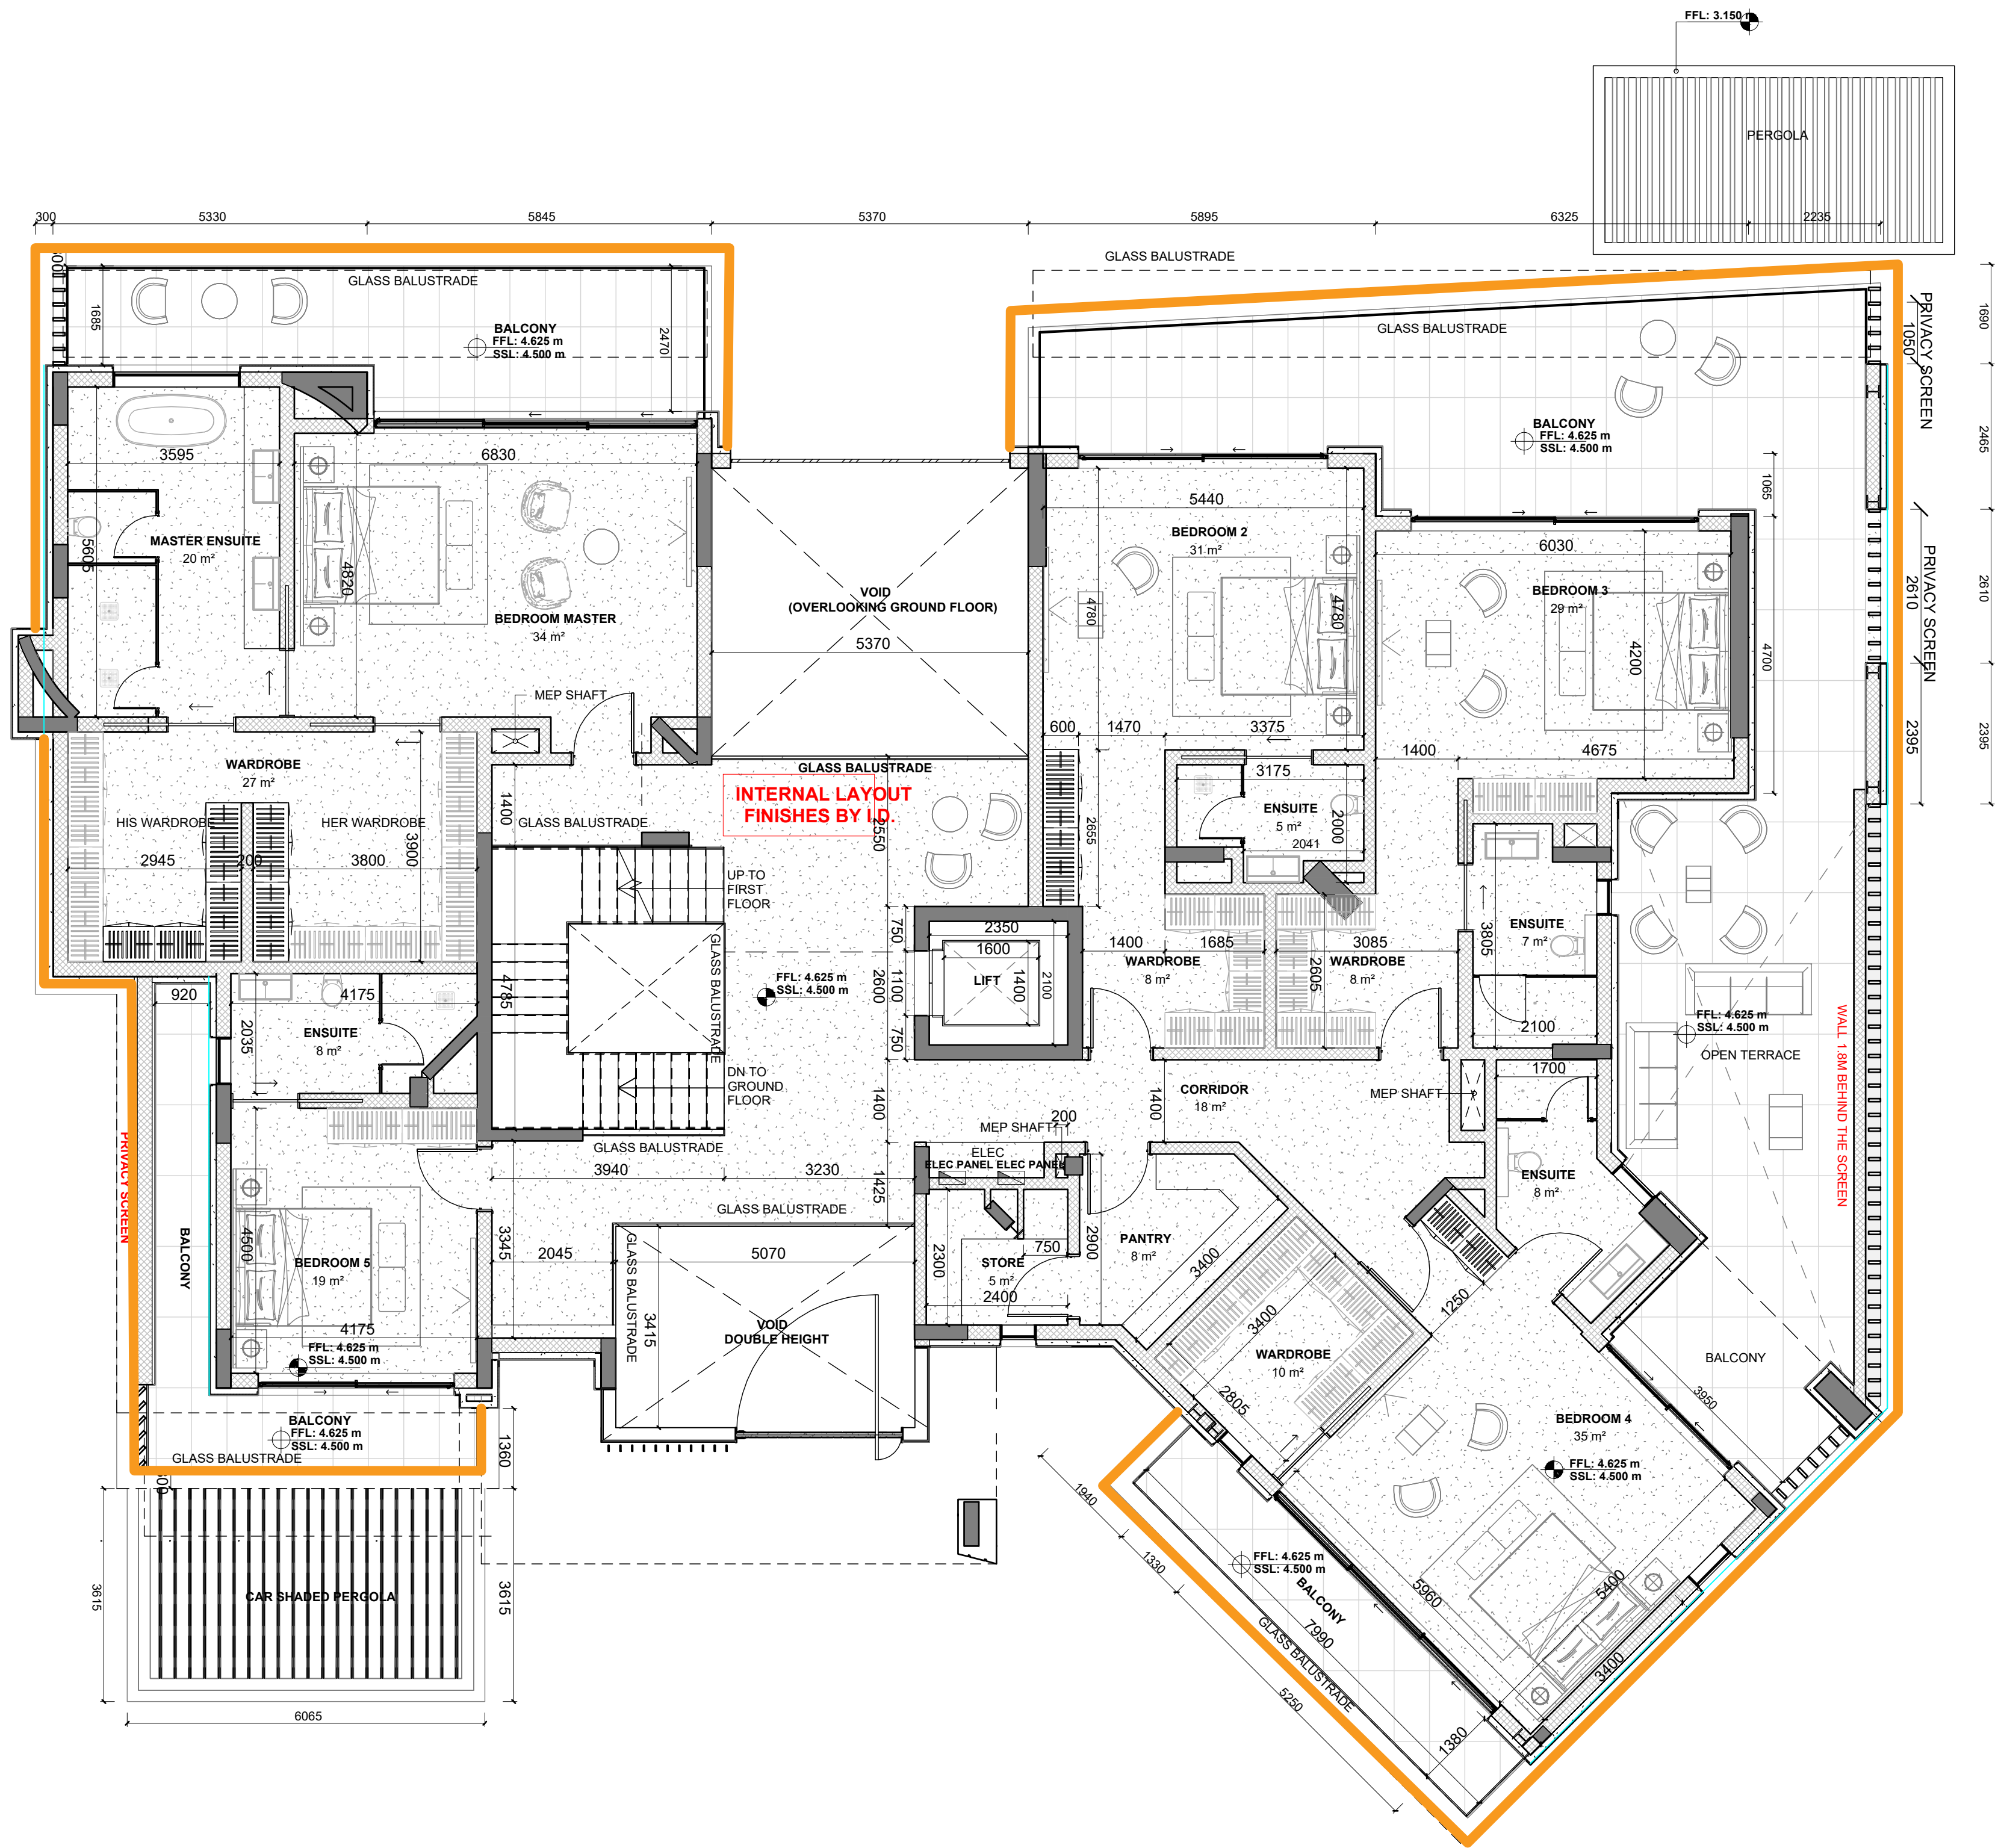

KEY PLAN

GENERAL NOTES

- THIS DRAWING IS NOT TO BE SCALED. THE STATED DIMENSIONS ONLY ARE TO BE CONSIDERED.
- FOR THE GENERAL NOTES & STANDARD DETAILS
- ALL DIMENSIONS ARE IN MILLIMETERS AND LEVELS ARE IN METER UNLESS OTHERWISE NOTED.
- SITE DIMENSION VERIFICATION REQUIRED PRIOR TO PRODUCTION.
- ALL FINISHES AND IRONMONGERIES AS PER APPROVED MATERIAL SAMPLES ONLY.
- ANY OBSERVED DISCREPANCY OF FINISHES AND DETAILS BETWEEN PROJECT DOCUMENTS (DRAWINGS, SPECIFICATION & BOQ), TO BE BROUGHT OUT TO DESIGNER FOR CONFIRMATION.

SHOP DRAWING/SUBMITTAL REVIEW

- ☐ STATUS A - APPROVED ☐ STATUS B - APPROVED WITH CHANGES / NOTES
- ☐ STATUS C - REVISED AND RESUBMIT ☐ STATUS D - REJECTED

SUBMITTAL WAS REVIEWED FOR DESIGN CONFORMITY, SPECIFICATION AND GENERAL CONFORMITY IN ACCORDANCE TO CONTRACT DOCUMENTS.

COMMENTS:

BY: DATE:

DRAWING REFERENCE

DWG. NO.	REV. NO.	DESCRIPTION

ISSUES

No.	Date	By	Revision Details

CLIENT
DAVID VON ROSEN VON
HOEWEL

PROJECT
L117 - PALM JUMEIRAH

PLOT NO.: P.FRL117 LOCATION: PALM JUMEIRAH BLOCK: PALM JUMEIRAH

CONSULTANT:

ORIENT CROWN
ARCHITECTURAL

MAIN CONTRACTOR:
OLSEN & PARTNERS
INTERIORS
P.O. BOX: 283025, DUBAI U.A.E.
TEL: +971 4 5516500,
FAX: +971 4 5516501
email: info@opimena.com
www.opimena.com

DRAWING TITLE


FIRST FLOOR PLAN

Drawn by Prepared by Checked by Approved by

File Ref. Date 02/09/2024 Scale AS SHOWN Revision 13

Drawing No.

CLADDING LEGEND (STONE & MARBLE)		
SYMBOL	DESCRIPTION	MATERIAL
	Crown	Travertine

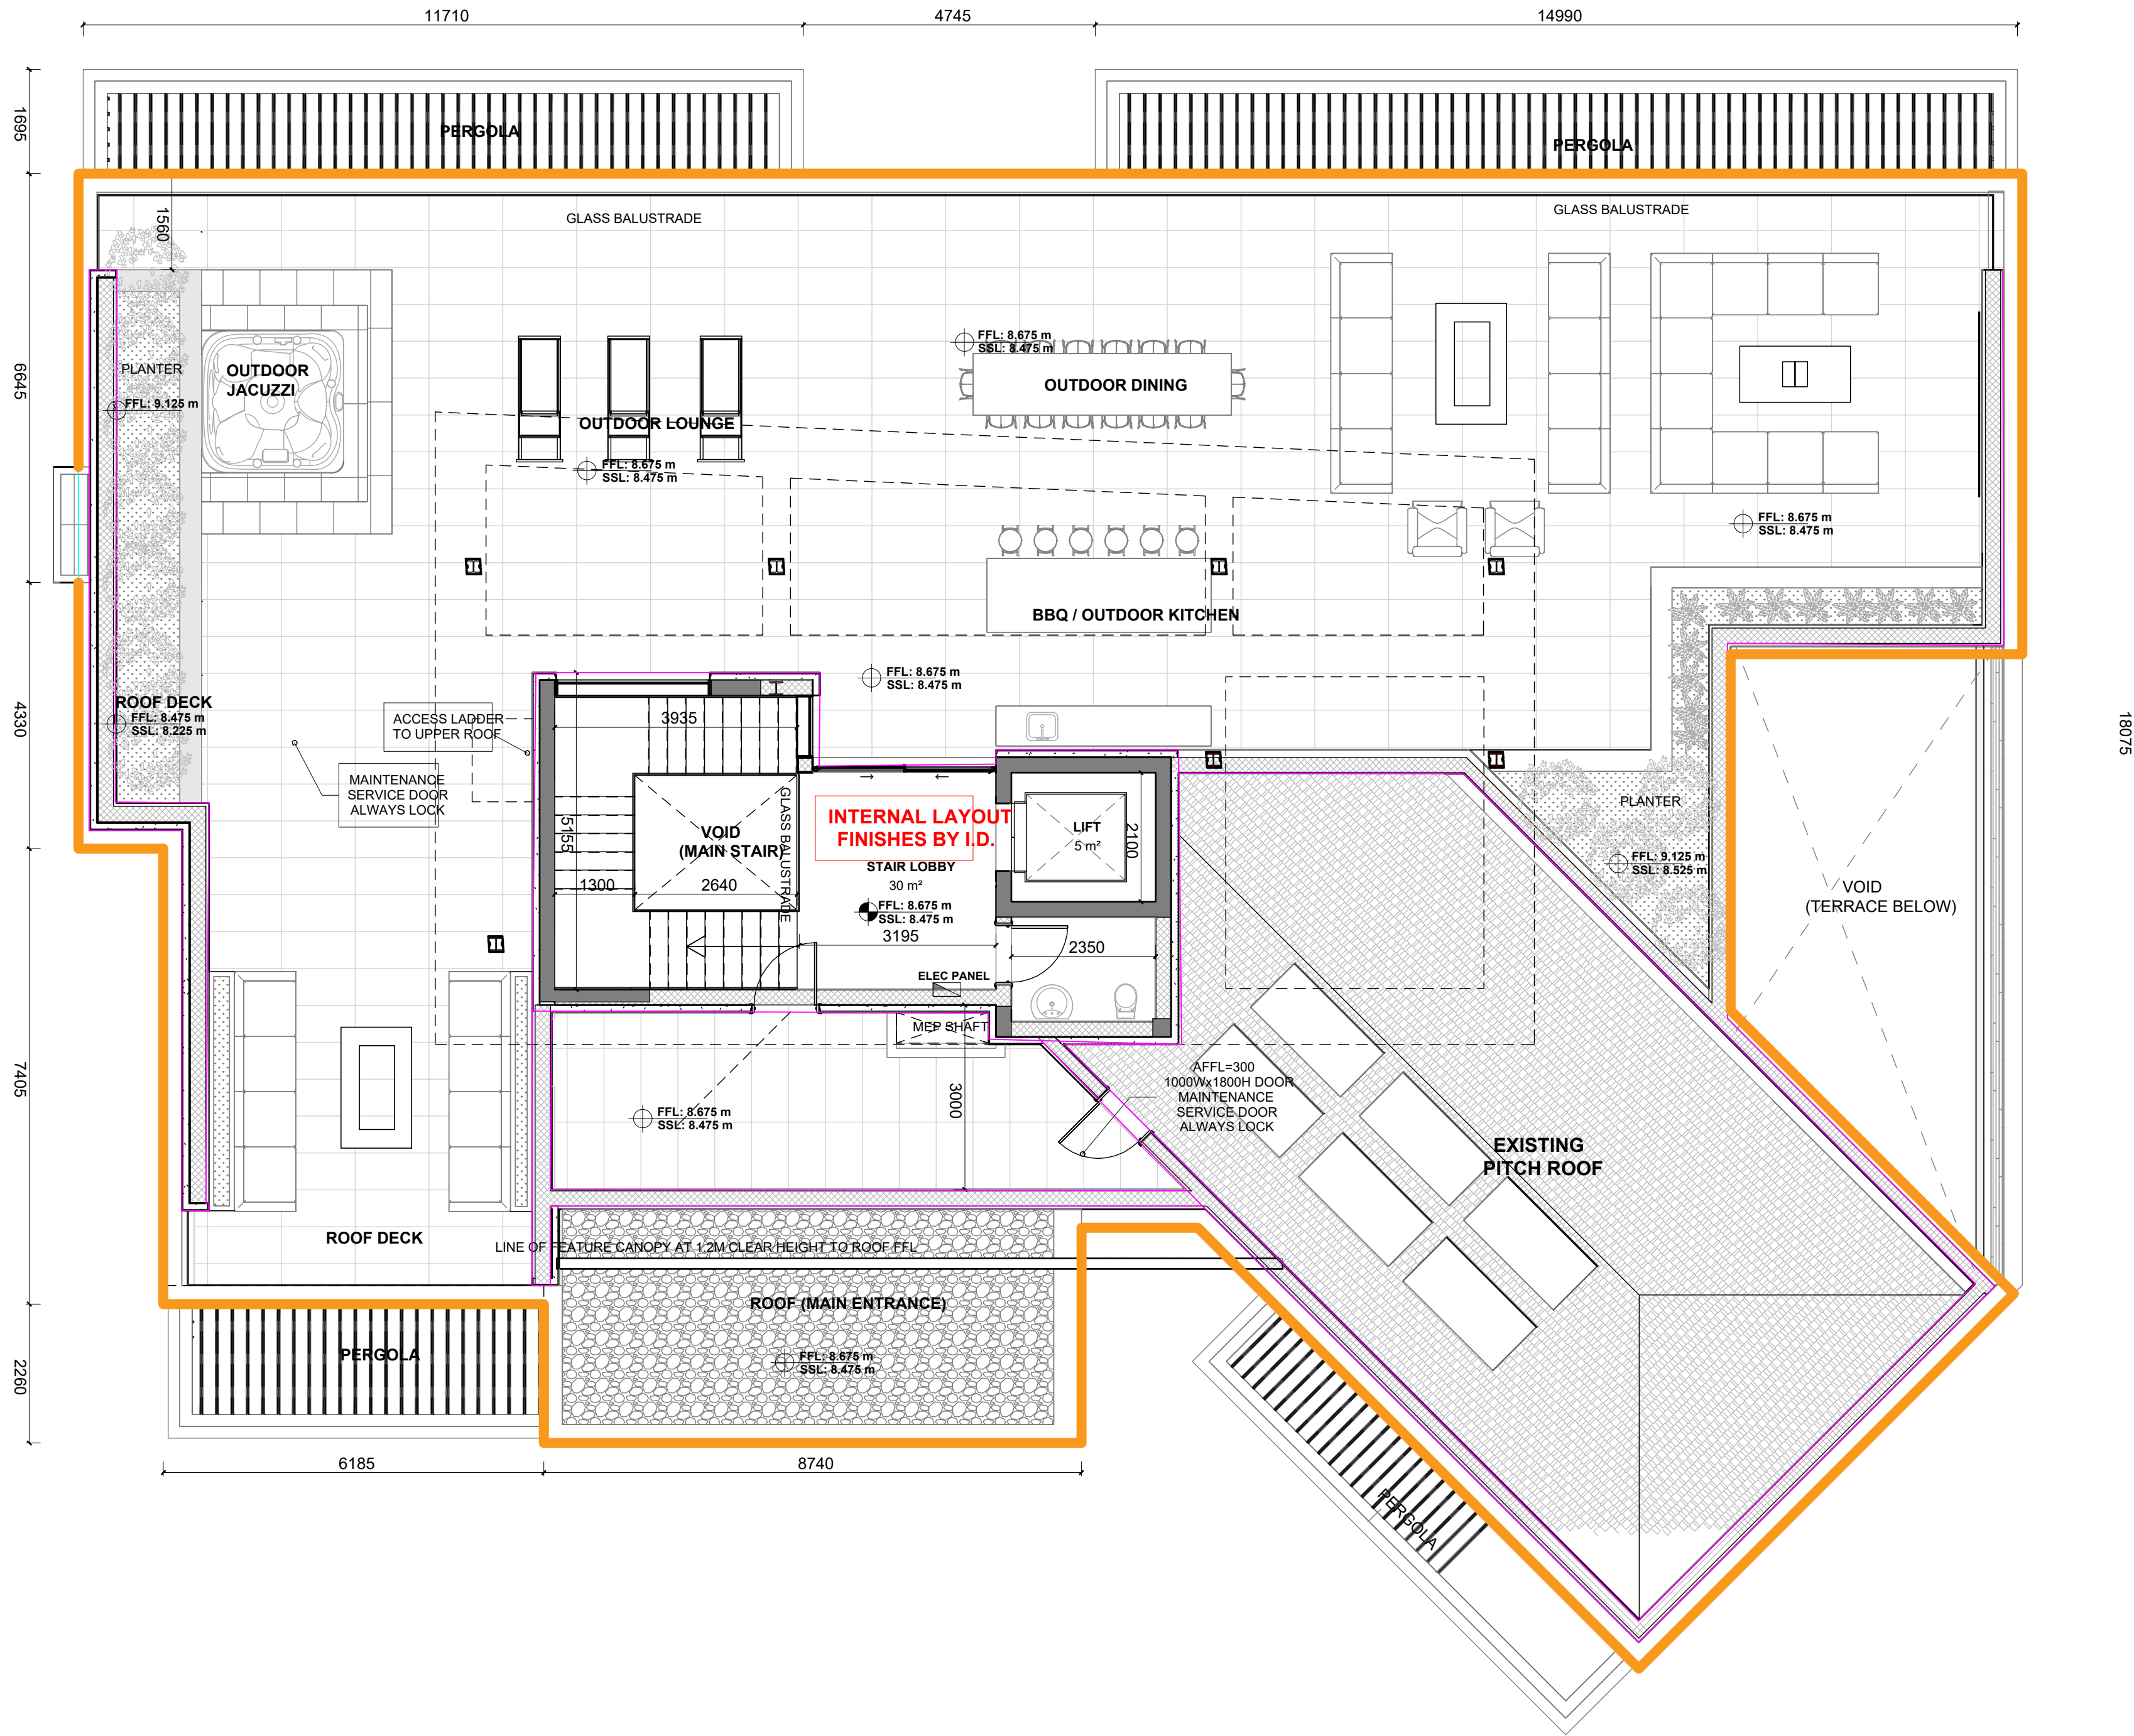

KEY PLAN

GENERAL NOTES

- THIS DRAWING IS NOT TO BE SCALED. THE STATED DIMENSIONS ONLY ARE TO BE CONSIDERED.
- FOR THE GENERAL NOTES & STANDARD DETAILS
- ALL DIMENSIONS ARE IN MILLIMETERS AND LEVELS ARE IN METER UNLESS OTHERWISE NOTED.
- SITE DIMENSION VERIFICATION REQUIRED PRIOR TO PRODUCTION.
- ALL FINISHES AND IRONMONGERIES AS PER APPROVED MATERIAL SAMPLES ONLY.
- ANY OBSERVED DISCREPANCY OF FINISHES AND DETAILS BETWEEN PROJECT DOCUMENTS (DRAWINGS, SPECIFICATION & BOQ), TO BE BROUGHT OUT TO DESIGNER FOR CONFIRMATION.

SHOP DRAWING/SUBMITTAL REVIEW

- | | |
|--|---|
| ☐ STATUS A - APPROVED | ☐ STATUS B - APPROVED WITH CHANGES / NOTES |
| ☐ STATUS C - REVISED AND RESUBMIT | ☐ STATUS D - REJECTED |

SUBMITTAL WAS REVIEWED FOR DESIGN CONFORMITY, SPECIFICATION AND GENERAL CONFORMITY IN ACCORDANCE TO CONTRACT DOCUMENTS.

COMMENTS:

BY:..... DATE:.....

DRAWING REFERENCE

DWG. NO.	REV. NO.	DESCRIPTION

ISSUES

No.	Date	By	Revision Details

CLIENT

DAVID VON ROSEN VON HOEWEL

PROJECT

L117 - PALM JUMEIRAH

PLOT NO.:	LOCATION:	BLOCK:
PJRL117	PALM JUMEIRAH	PALM JUMEIRAH

CONSULTANT:



MAIN CONTRACTOR:

OLSEN & PARTNERS
INTERIORS
P.O. BOX: 283025, DUBAI U.A.E.
TEL: +971 4 5516500,
FAX: +971 4 5516501
email: info@opimena.com
www.opimena.com


DRAWING TITLE

ROOF FLOOR PLAN

Drawn by	Prepared by	Checked by	Approved by
----------	-------------	------------	-------------


File Ref.	Date	Scale	Revision
	02/09/2024	AS SHOWN	13

Drawing No.

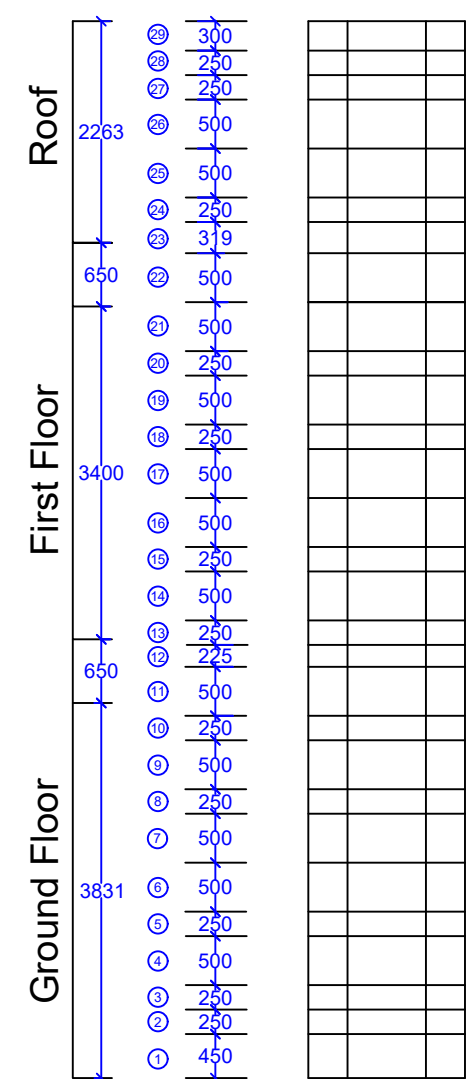

Parapet groove size is:
20mm width, 5mm depth


Parapet groove size is:
20mm width, 5mm depth

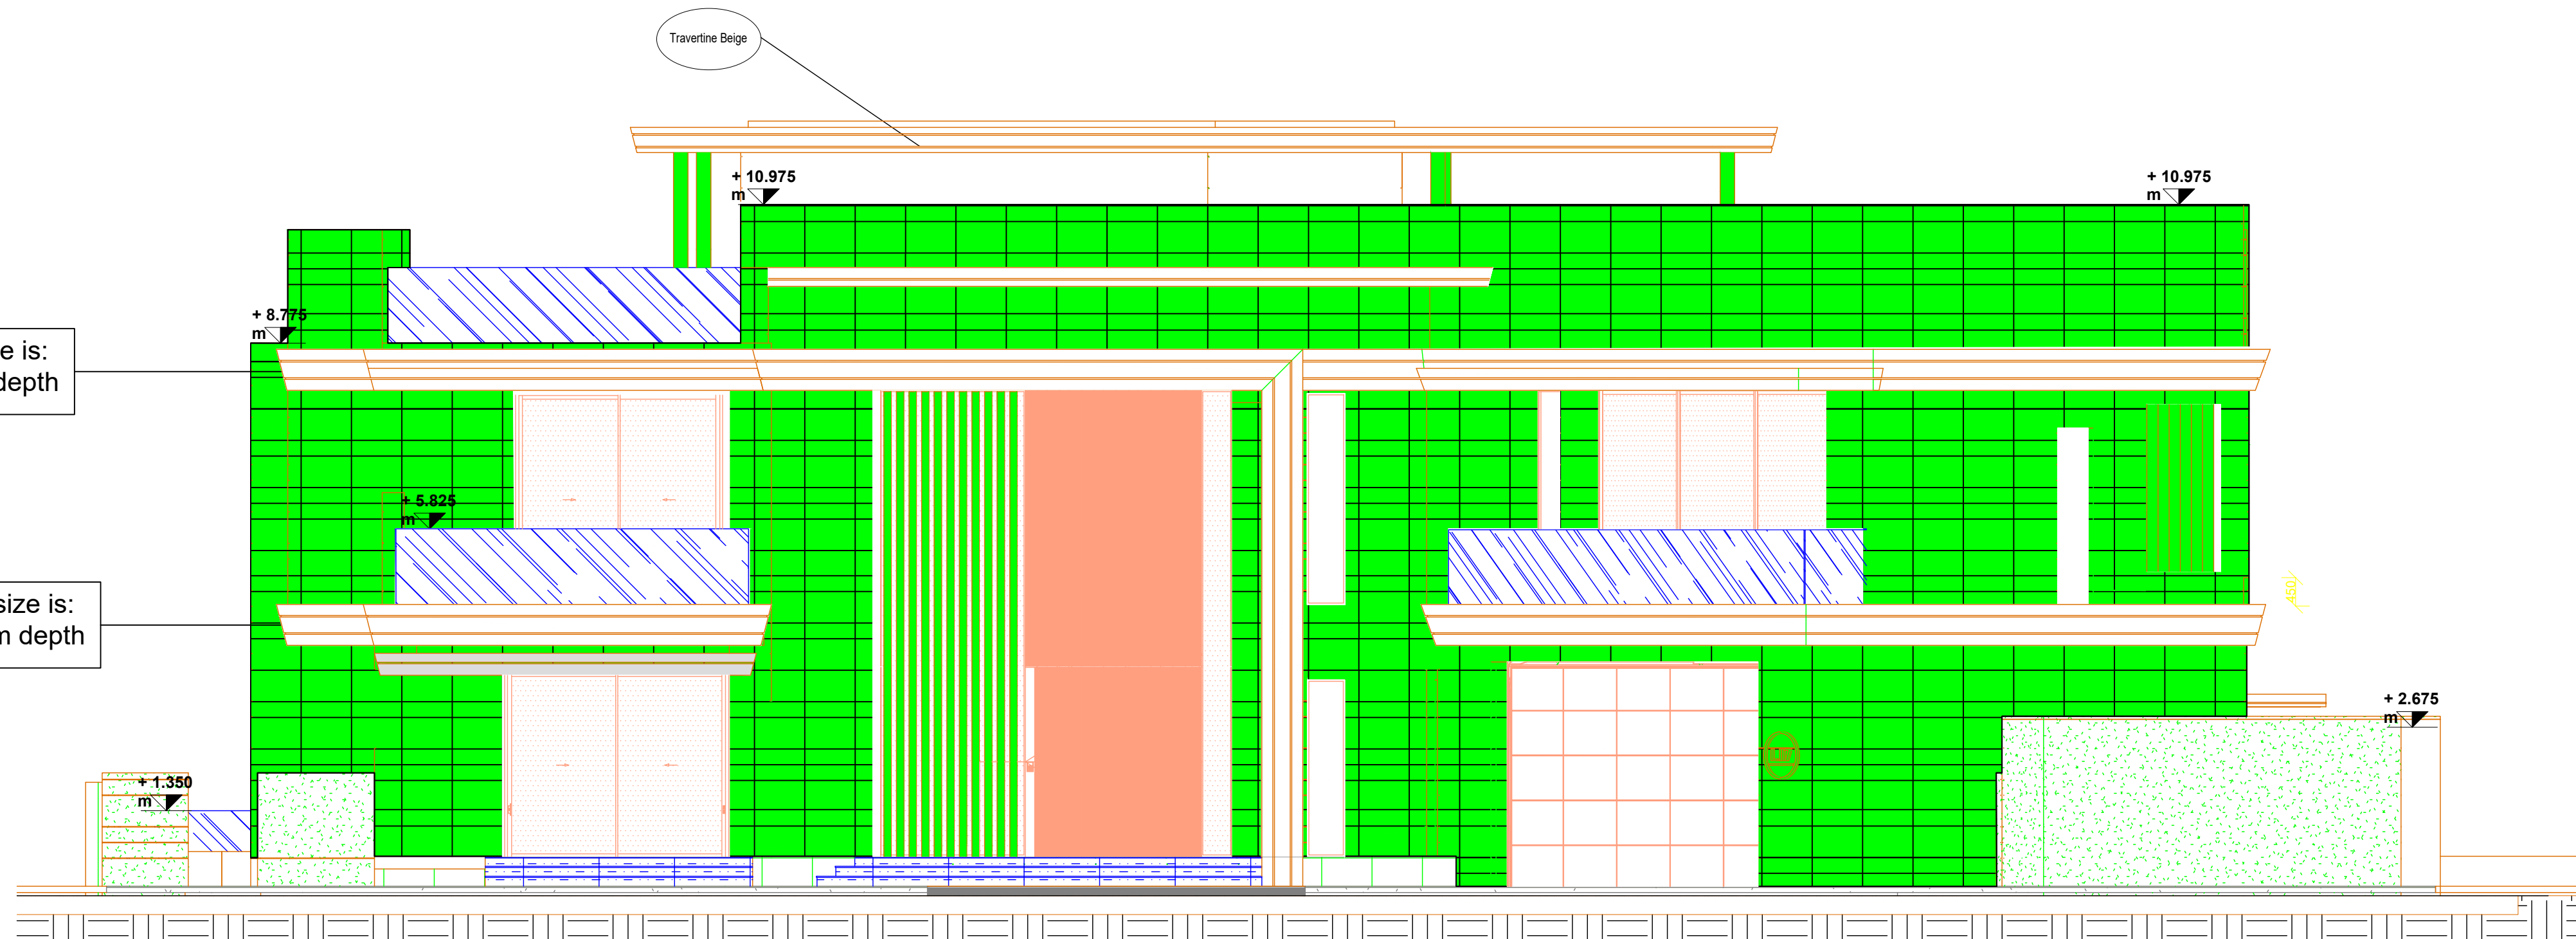

1 FRONT ELEVATION-A

SCALE 1:100


All horizontal joints width is 5mm as per system pin diameter with
Groove size : 10mm width, 10mm depth
Vertical joints width is 2mm
Corner details to be 5mm machine cut.

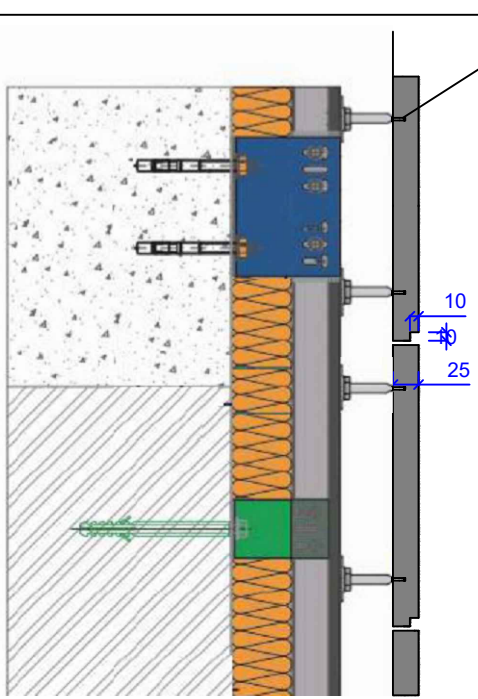

Supported with glue as per approved mockup


FIXED FINISHES LEGEND

A.415	Artificial Stone
A.416	Artificial Stone
	Travertine Beige for Parapet

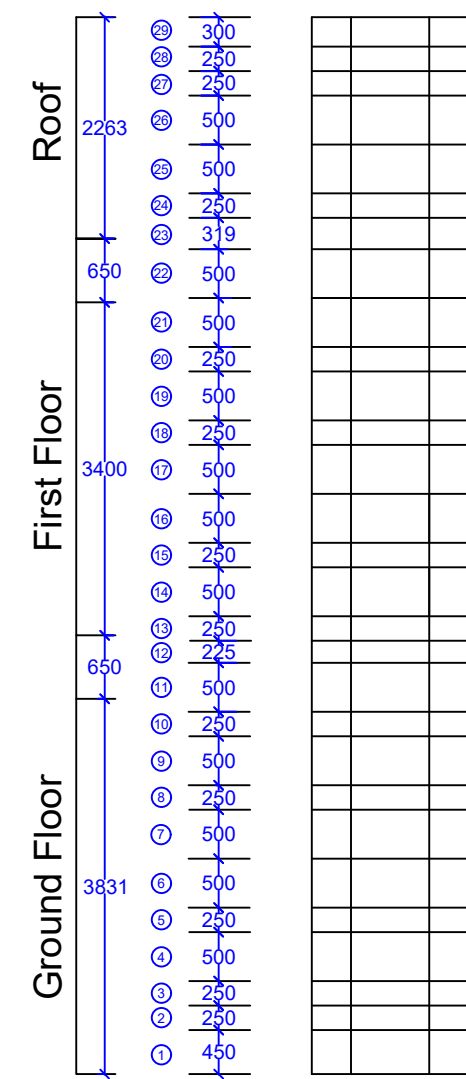

Parapet groove size is:
20mm width, 5mm depth

Parapet groove size is:
20mm width, 5mm depth

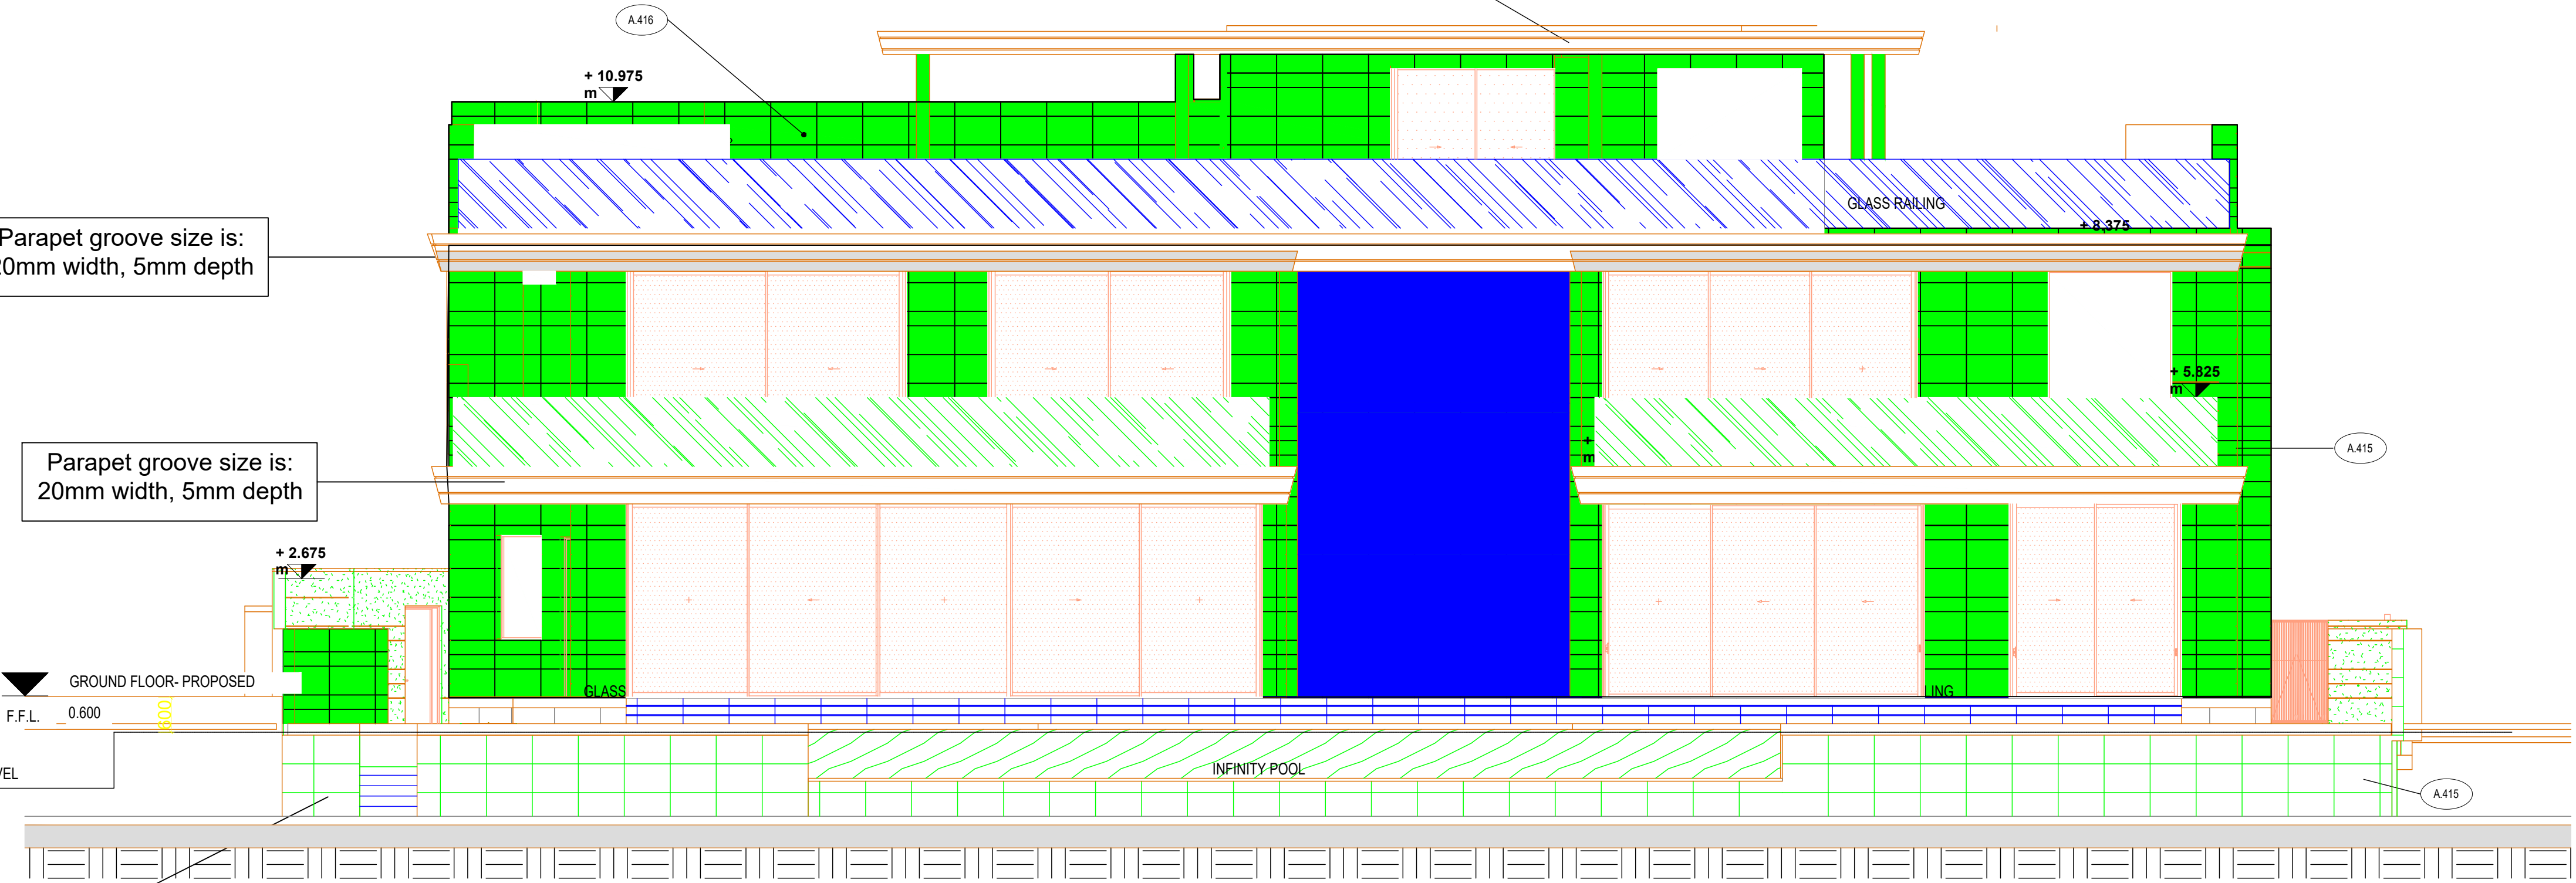

2 REAR ELEVATION-B

SCALE 1:100

KEY PLAN

GENERAL NOTES

- THIS DRAWING IS NOT TO BE SCALED. THE STATED DIMENSIONS ONLY ARE TO BE CONSIDERED.
- FOR THE GENERAL NOTES & STANDARD DETAILS
- ALL DIMENSIONS ARE IN MILLIMETERS AND LEVELS ARE IN METER UNLESS OTHERWISE NOTED.
- SITE DIMENSION VERIFICATION REQUIRED PRIOR TO PRODUCTION.
- ALL FINISHES AND IRONMONGERIES AS PER APPROVED MATERIAL SAMPLES ONLY.
- ANY OBSERVED DISCREPANCY OF FINISHES AND DETAILS BETWEEN PROJECT DOCUMENTS (DRAWINGS, SPECIFICATION & BOQ), TO BE BROUGHT OUT TO DESIGNER FOR CONFIRMATION.

SHOP DRAWING/SUBMITTAL REVIEW

- | | |
|--|---|
| ☐ STATUS A - APPROVED | ☐ STATUS B - APPROVED WITH CHANGES / NOTES |
| ☐ STATUS C - REVISED AND RESUBMIT | ☐ STATUS D - REJECTED |

SUBMITTAL WAS REVIEWED FOR DESIGN CONFORMITY, SPECIFICATION AND GENERAL CONFORMITY IN ACCORDANCE TO CONTRACT DOCUMENTS.

COMMENTS:

BY:..... DATE:.....

DRAWING REFERENCE

DWG. NO.	REV. NO.	DESCRIPTION

ISSUES

No.	Date	By	Revision Details

CLIENT

DAVID VON ROSEN VON HOEWEL

PROJECT

L117 - PALM JUMEIRAH

PLOT NO.: P.FRL117 LOCATION: PALM JUMEIRAH BLOCK: PALM JUMEIRAH

CONSULTANT:

ORIENT CROWN
ARCHITECTURAL
TRADES & SERVICES CONSULTING LLC

MAIN CONTRACTOR:

OLSEN & PARTNERS
INTERIORS
P.O. BOX: 283025, DUBAI U.A.E.
TEL: +971 4 5516500,
FAX: +971 4 5516501
email: info@opimena.com
www.opimena.com


DRAWING TITLE

External cladding pattern drawings
(Option 2 25mm stone thickness with 10mm Groove)

Drawn by Prepared by Checked by Approved by

File Ref. Date 26/10/2024 Scale AS SHOWN Revision 17


Drawing No.

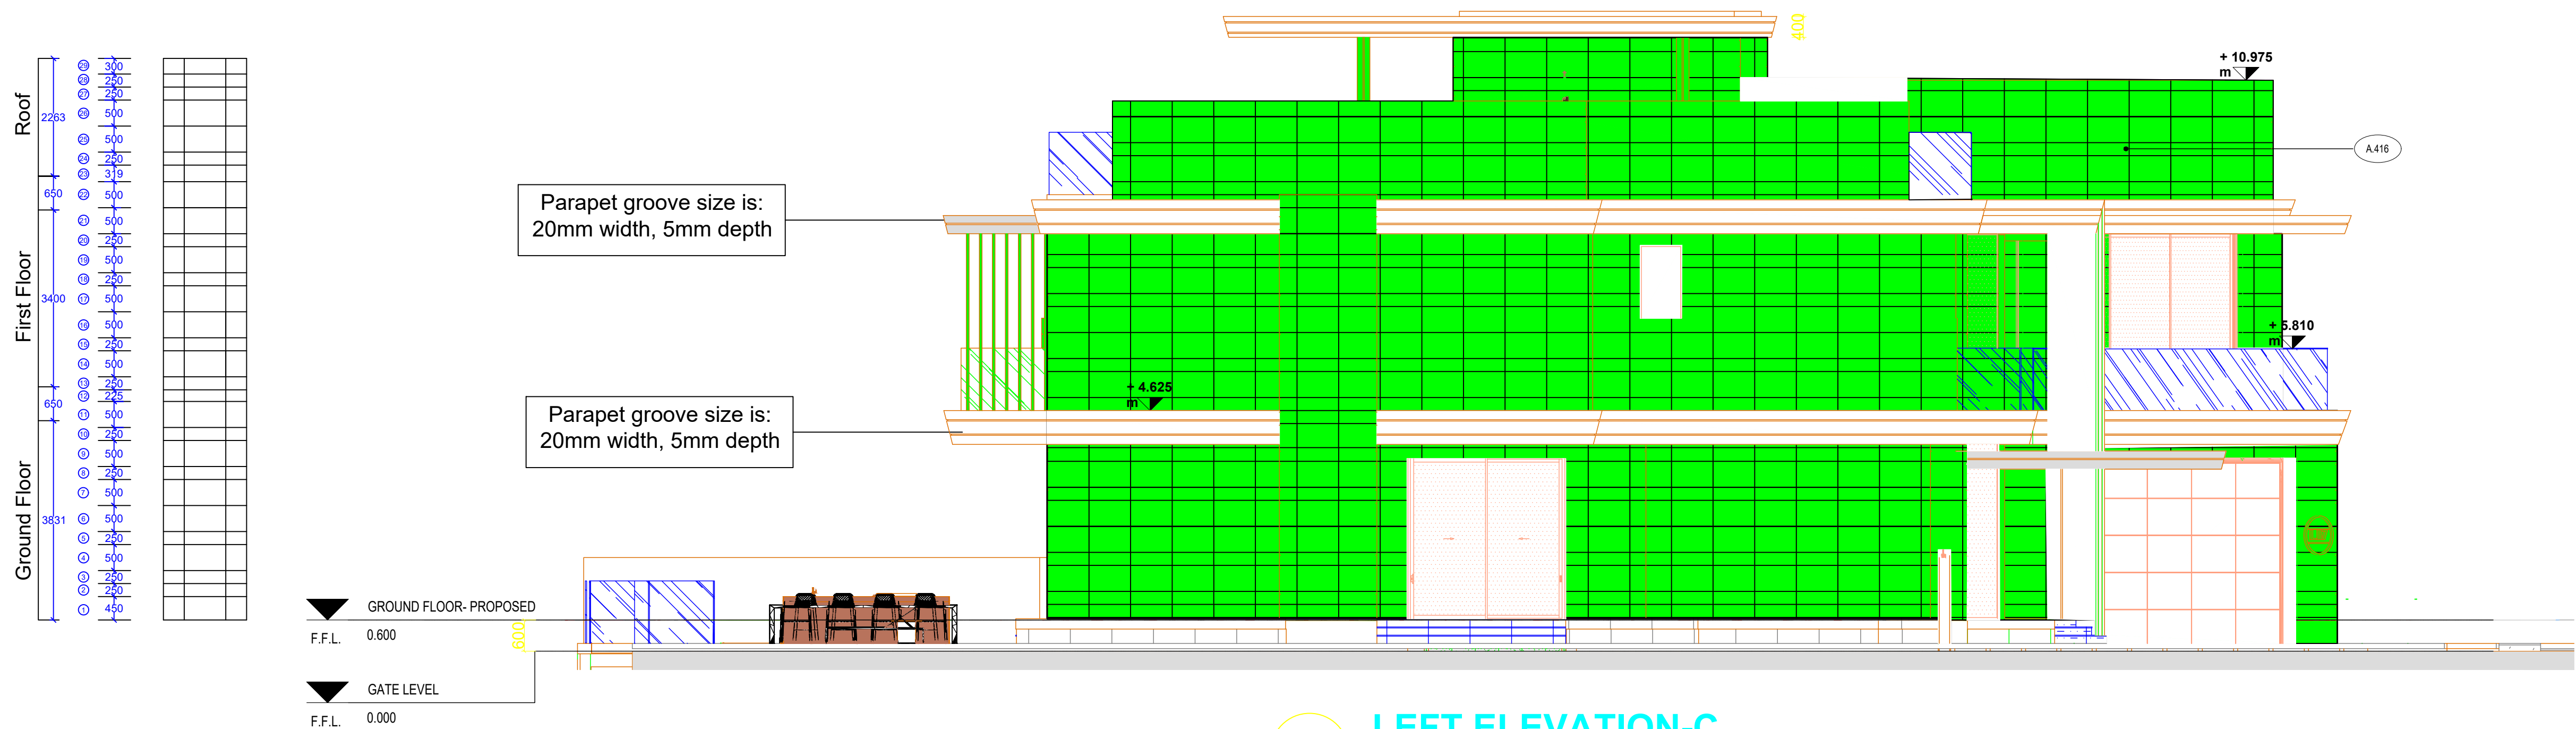

3 LEFT ELEVATION-C
SCALE 1:100

FIXED FINISHES LEGEND

A.415	Artificial Stone
A.416	Artificial Stone
	Travertine Beige for Parapet

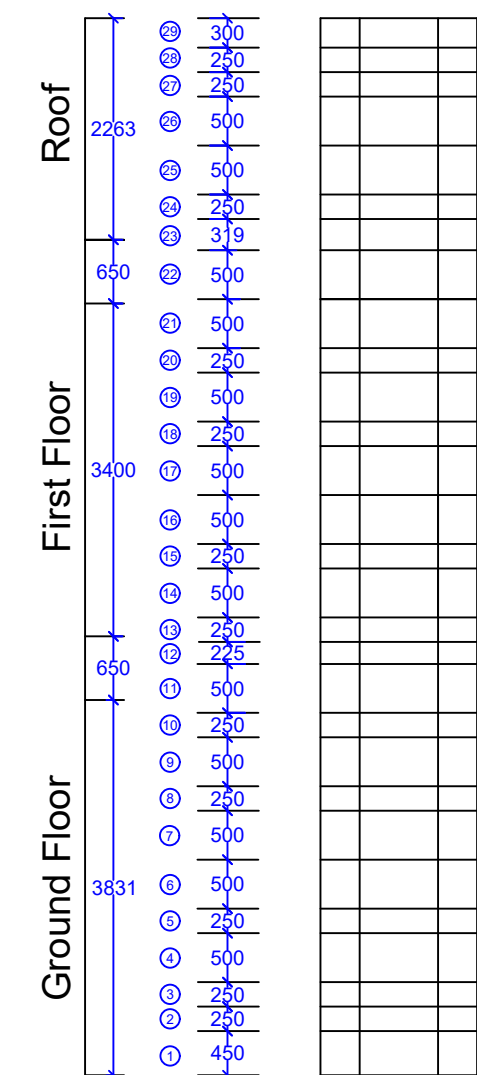

4 RIGHT ELEVATION-D
SCALE 1:100

KEY PLAN

GENERAL NOTES

1. THIS DRAWING IS NOT TO BE SCALED. THE STATED DIMENSIONS ONLY ARE TO BE CONSIDERED.
2. FOR THE GENERAL NOTES & STANDARD DETAILS ARE IN MILLIMETERS AND LEVELS ARE IN METER UNLESS OTHERWISE NOTED.
3. ALL DIMENSIONS ARE IN MILLIMETERS AND LEVELS ARE IN METER UNLESS OTHERWISE NOTED.
4. SITE DIMENSION VERIFICATION REQUIRED PRIOR TO PRODUCTION.
5. ALL FINISHES AND IRONMONGERIES AS PER APPROVED MATERIAL SAMPLES ONLY.
6. ANY OBSERVED DISCREPANCY OF FINISHES AND DETAILS BETWEEN PROJECT DOCUMENTS (DRAWINGS, SPECIFICATION & BOQ), TO BE BROUGHT OUT TO DESIGNER FOR CONFIRMATION.

SHOP DRAWING/SUBMITTAL REVIEW

- | | |
|--|---|
| ☐ STATUS A - APPROVED | ☐ STATUS B - APPROVED WITH CHANGES / NOTES |
| ☐ STATUS C - REVISED AND RESUBMIT | ☐ STATUS D - REJECTED |

SUBMITTAL WAS REVIEWED FOR DESIGN CONFORMITY, SPECIFICATION AND GENERAL CONFORMITY IN ACCORDANCE TO CONTRACT DOCUMENTS.

COMMENTS:

BY:..... DATE:.....

DRAWING REFERENCE

DWG. NO.	REV. NO.	DESCRIPTION

ISSUES

No.	Date	By	Revision Details

CLIENT

DAVID VON ROSEN VON HOEWEL

PROJECT

L117 - PALM JUMEIRAH

PLOT NO.: P/JRL117 LOCATION: PALM JUMEIRAH BLOCK: PALM JUMEIRAH

CONSULTANT:

ORIENT CROWN
ARCHITECTURAL
TRADEMARK & SERVICE TO BUILDING INDUSTRY

MAIN CONTRACTOR:

OLSEN & PARTNERS
INTERIORS
P.O. BOX: 283025, DUBAI U.A.E.
TEL: +971 4 5516500,
FAX: +971 4 5516501
email: info@opimena.com
www.opimena.com





DRAWING TITLE

External cladding pattern drawings
(Option 2 25mm stone thickness with 10mm Groove)

Drawn by	Prepared by	Checked by	Approved by

File Ref.	Date	Scale	Revision
	26/10/2024	AS SHOWN	17

Drawing No.

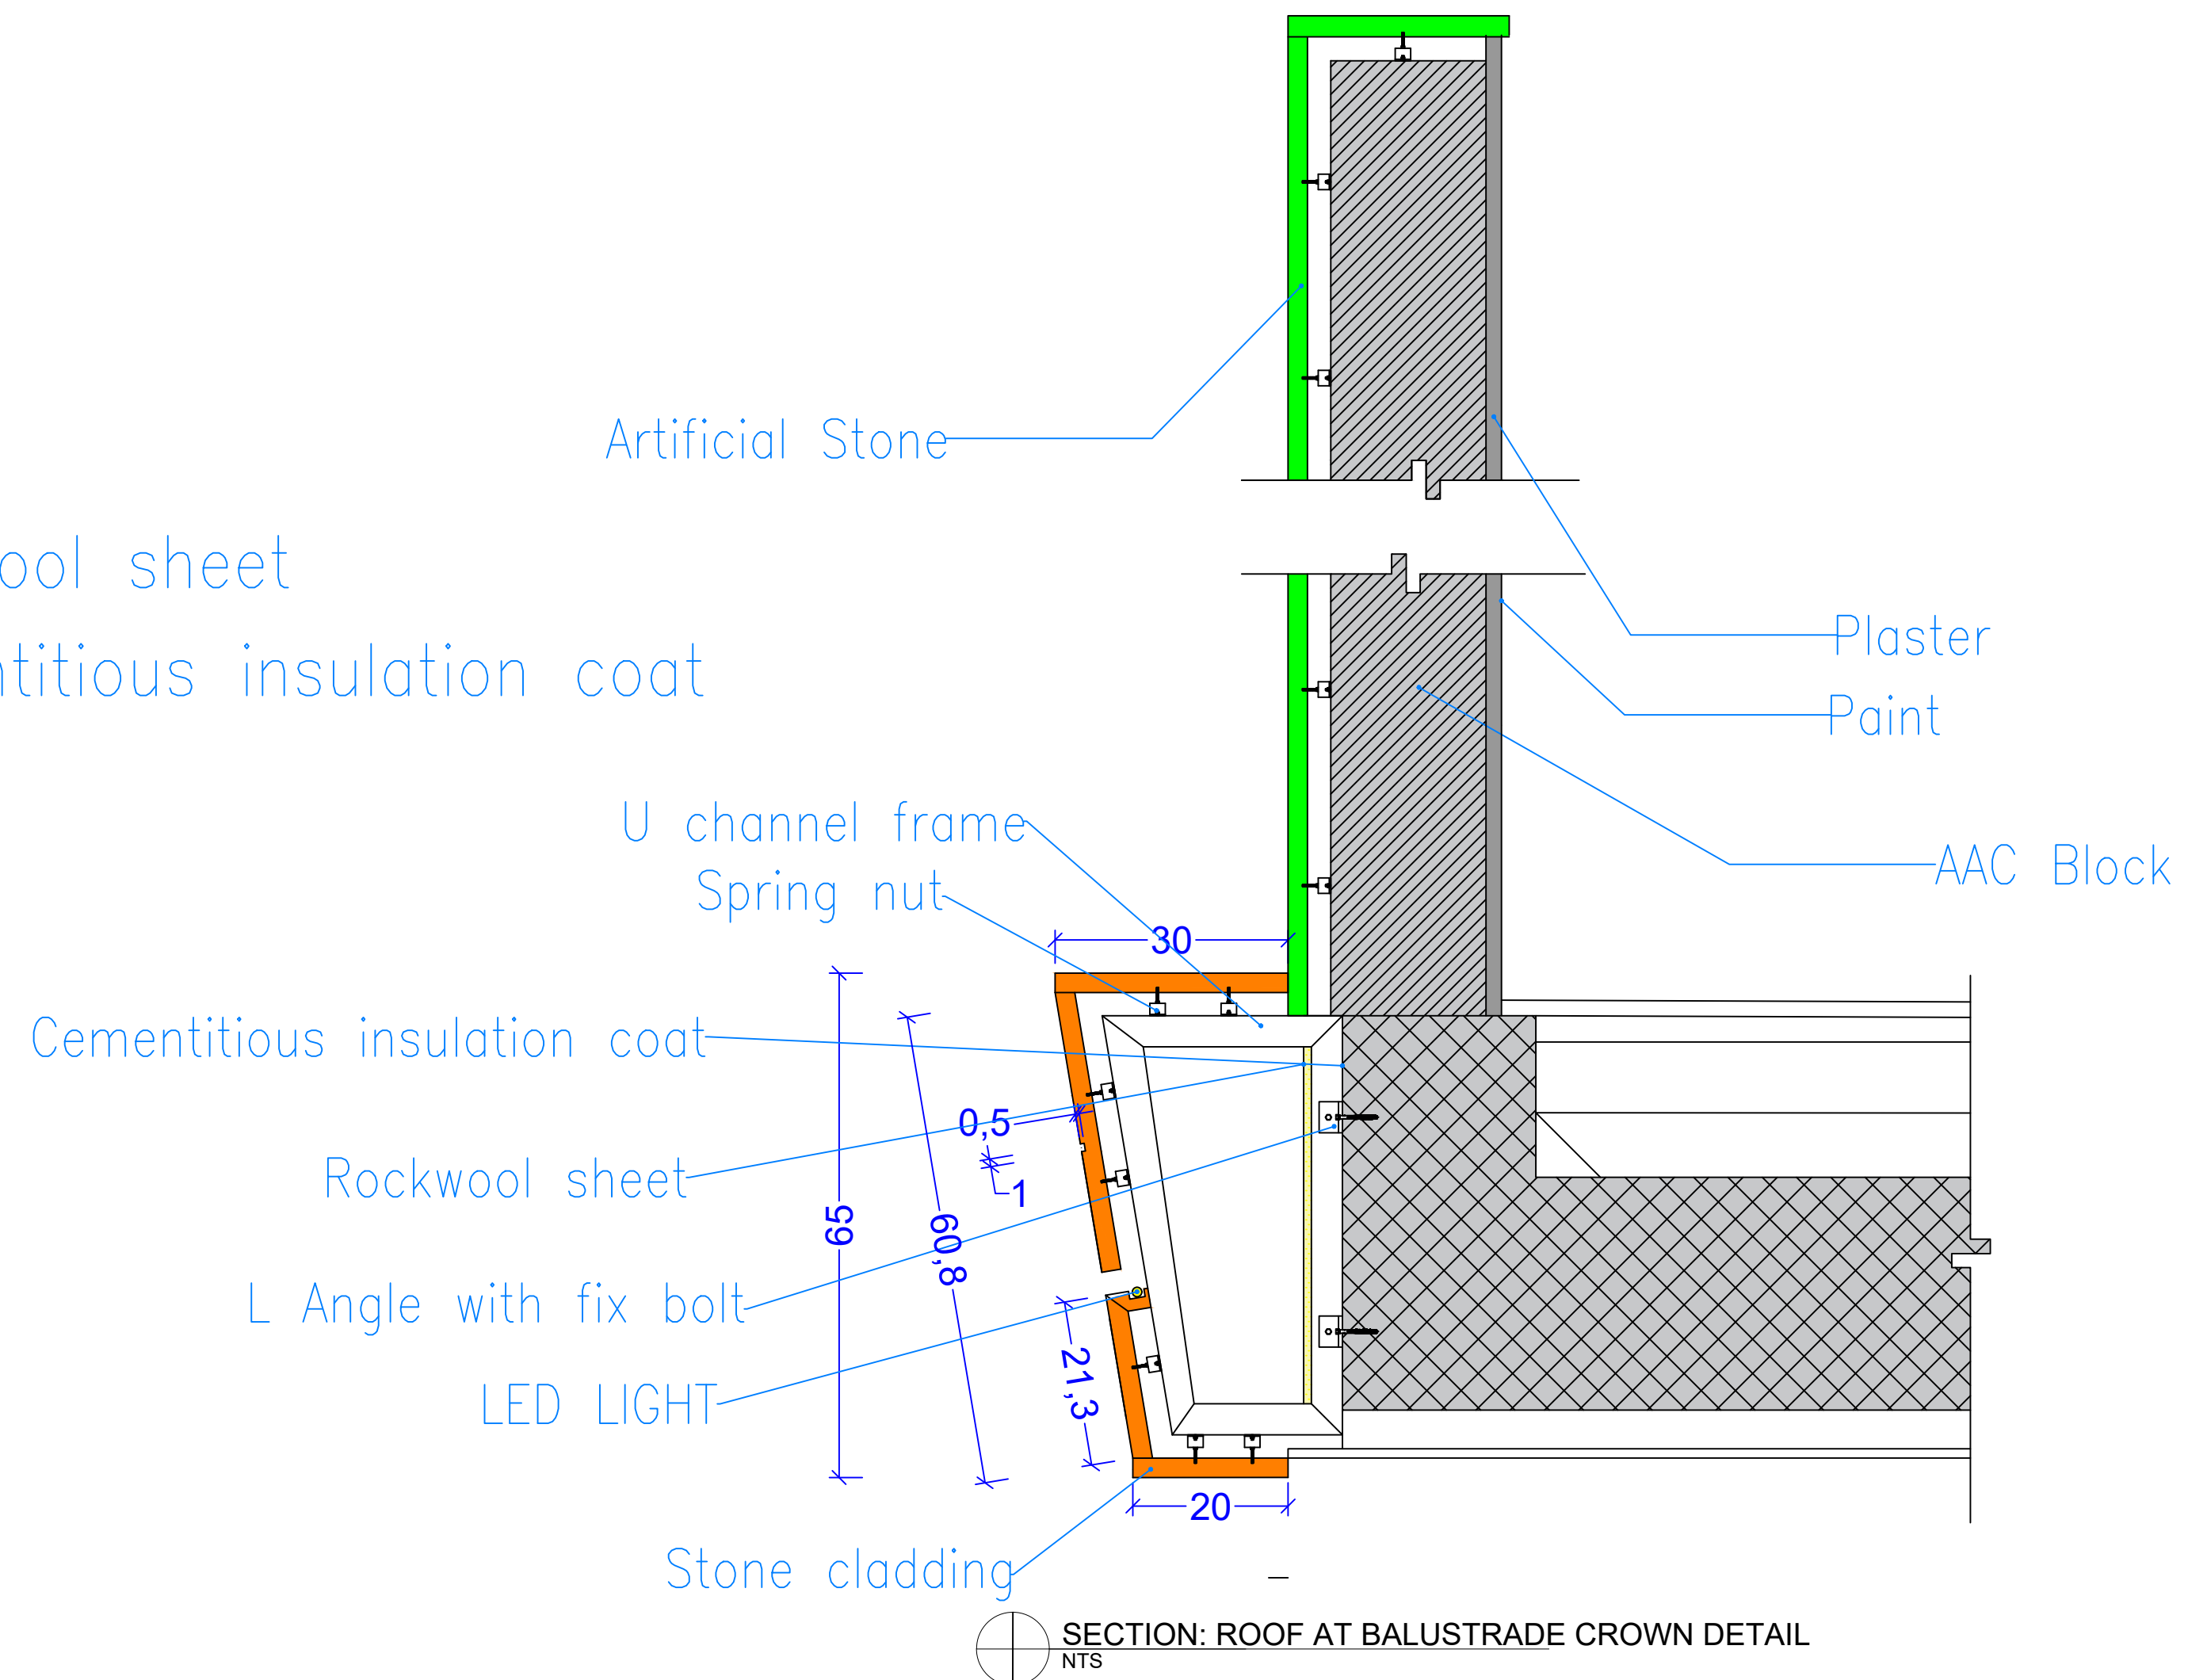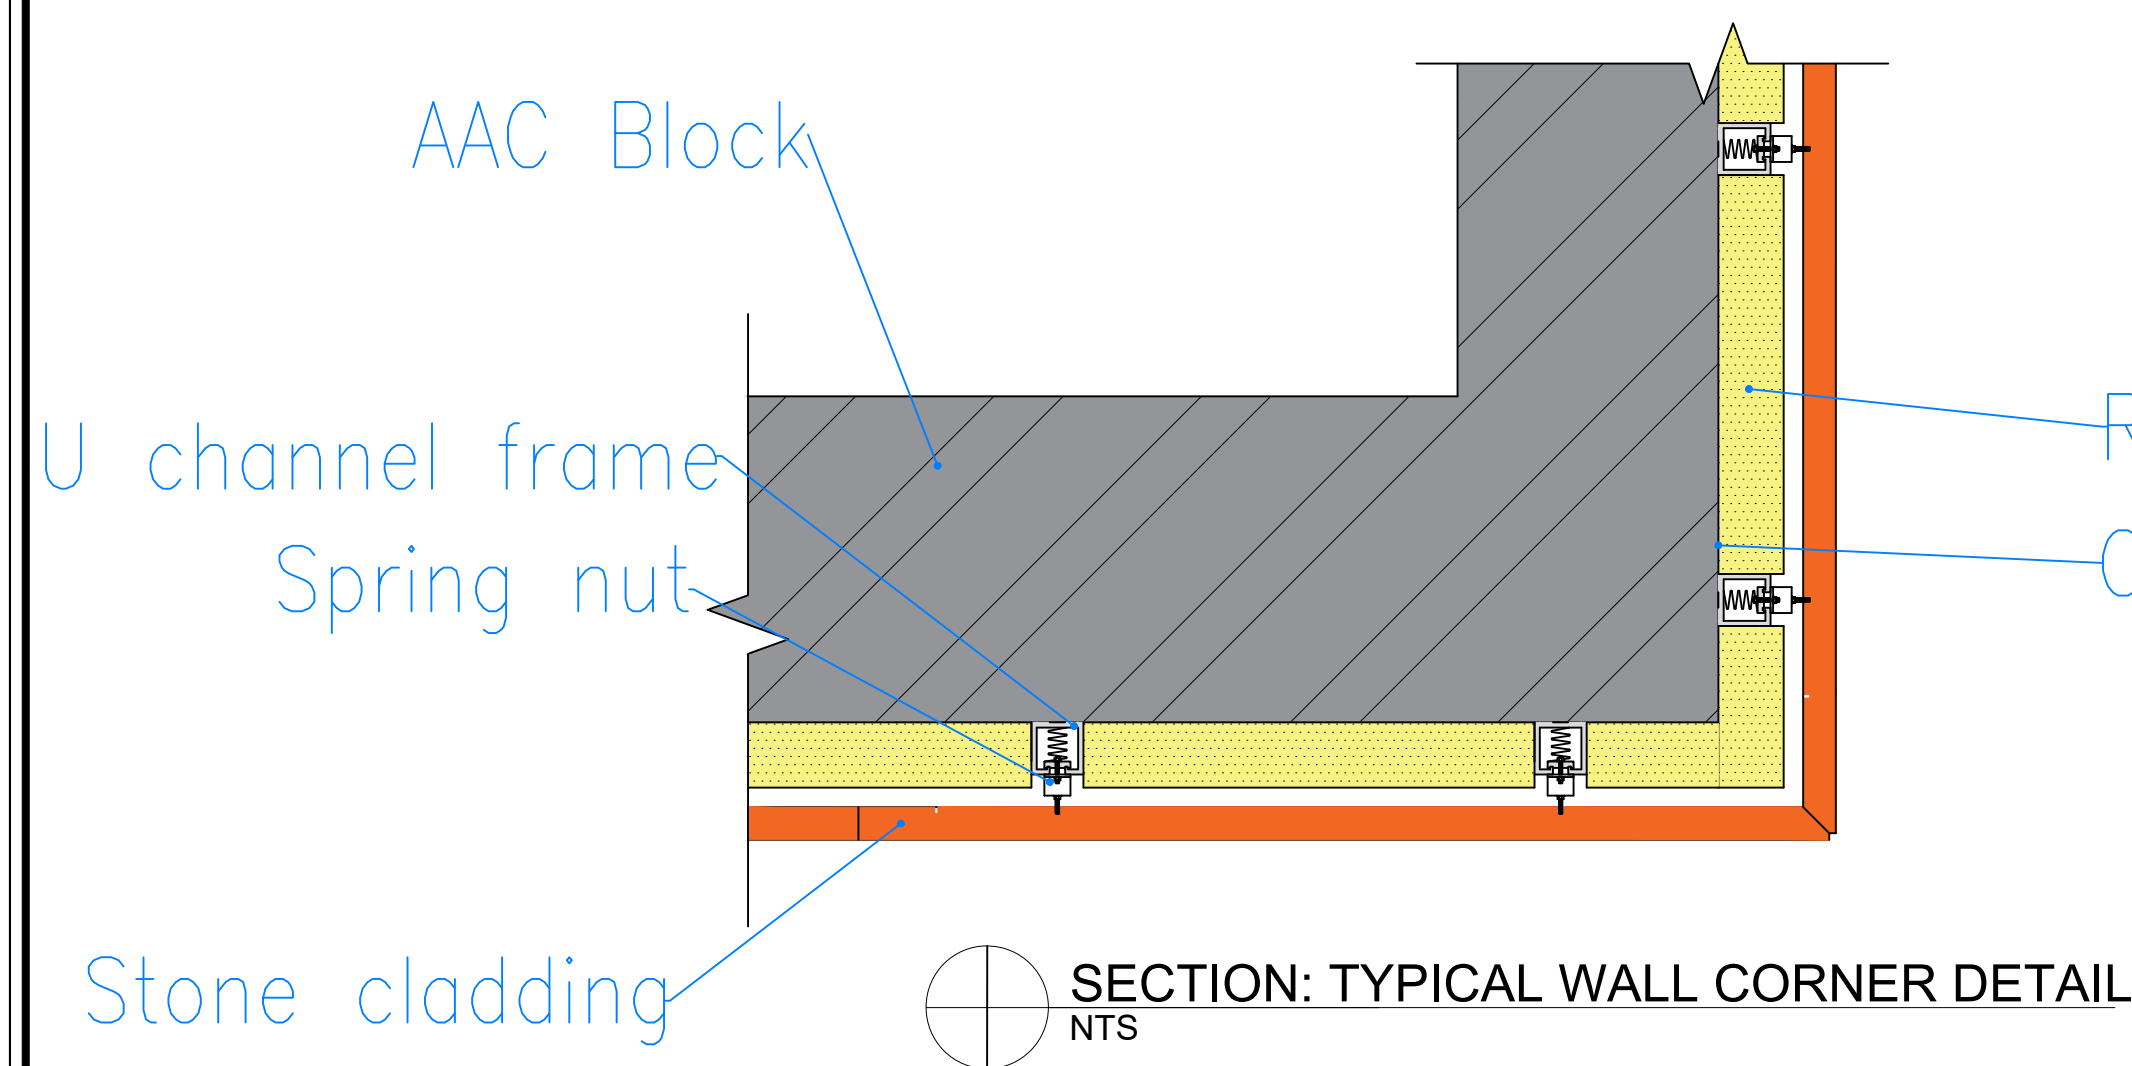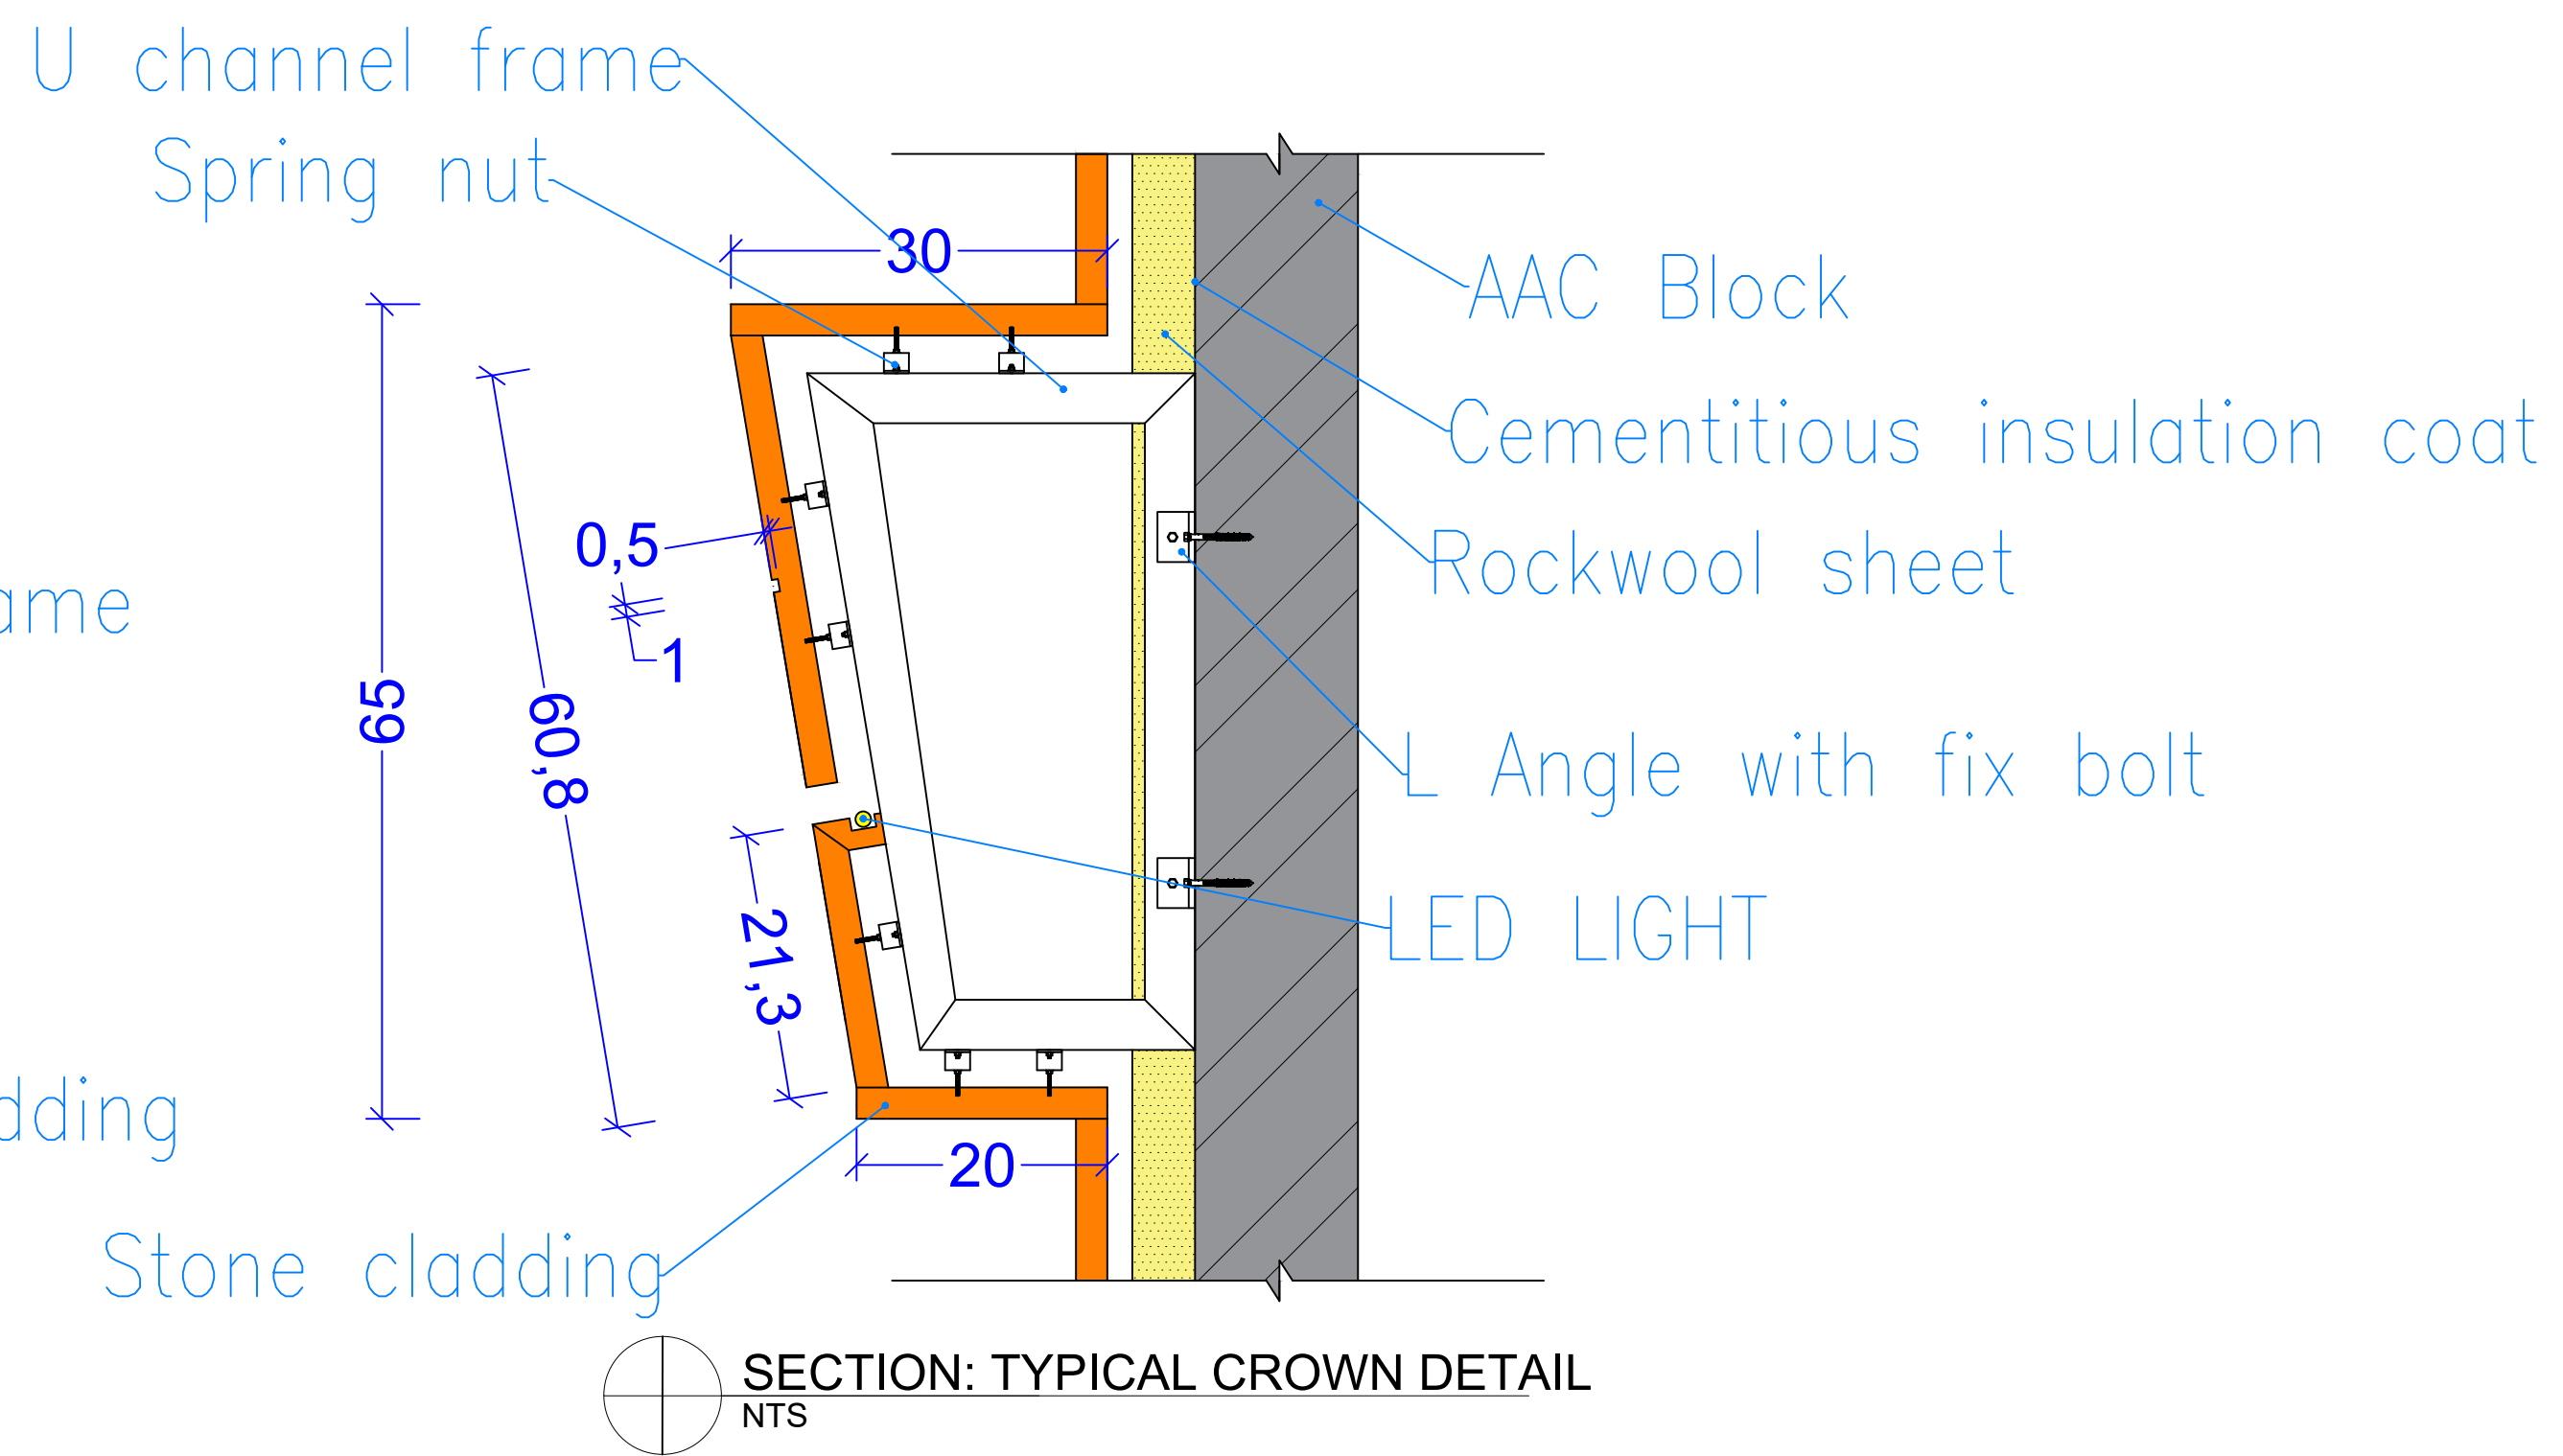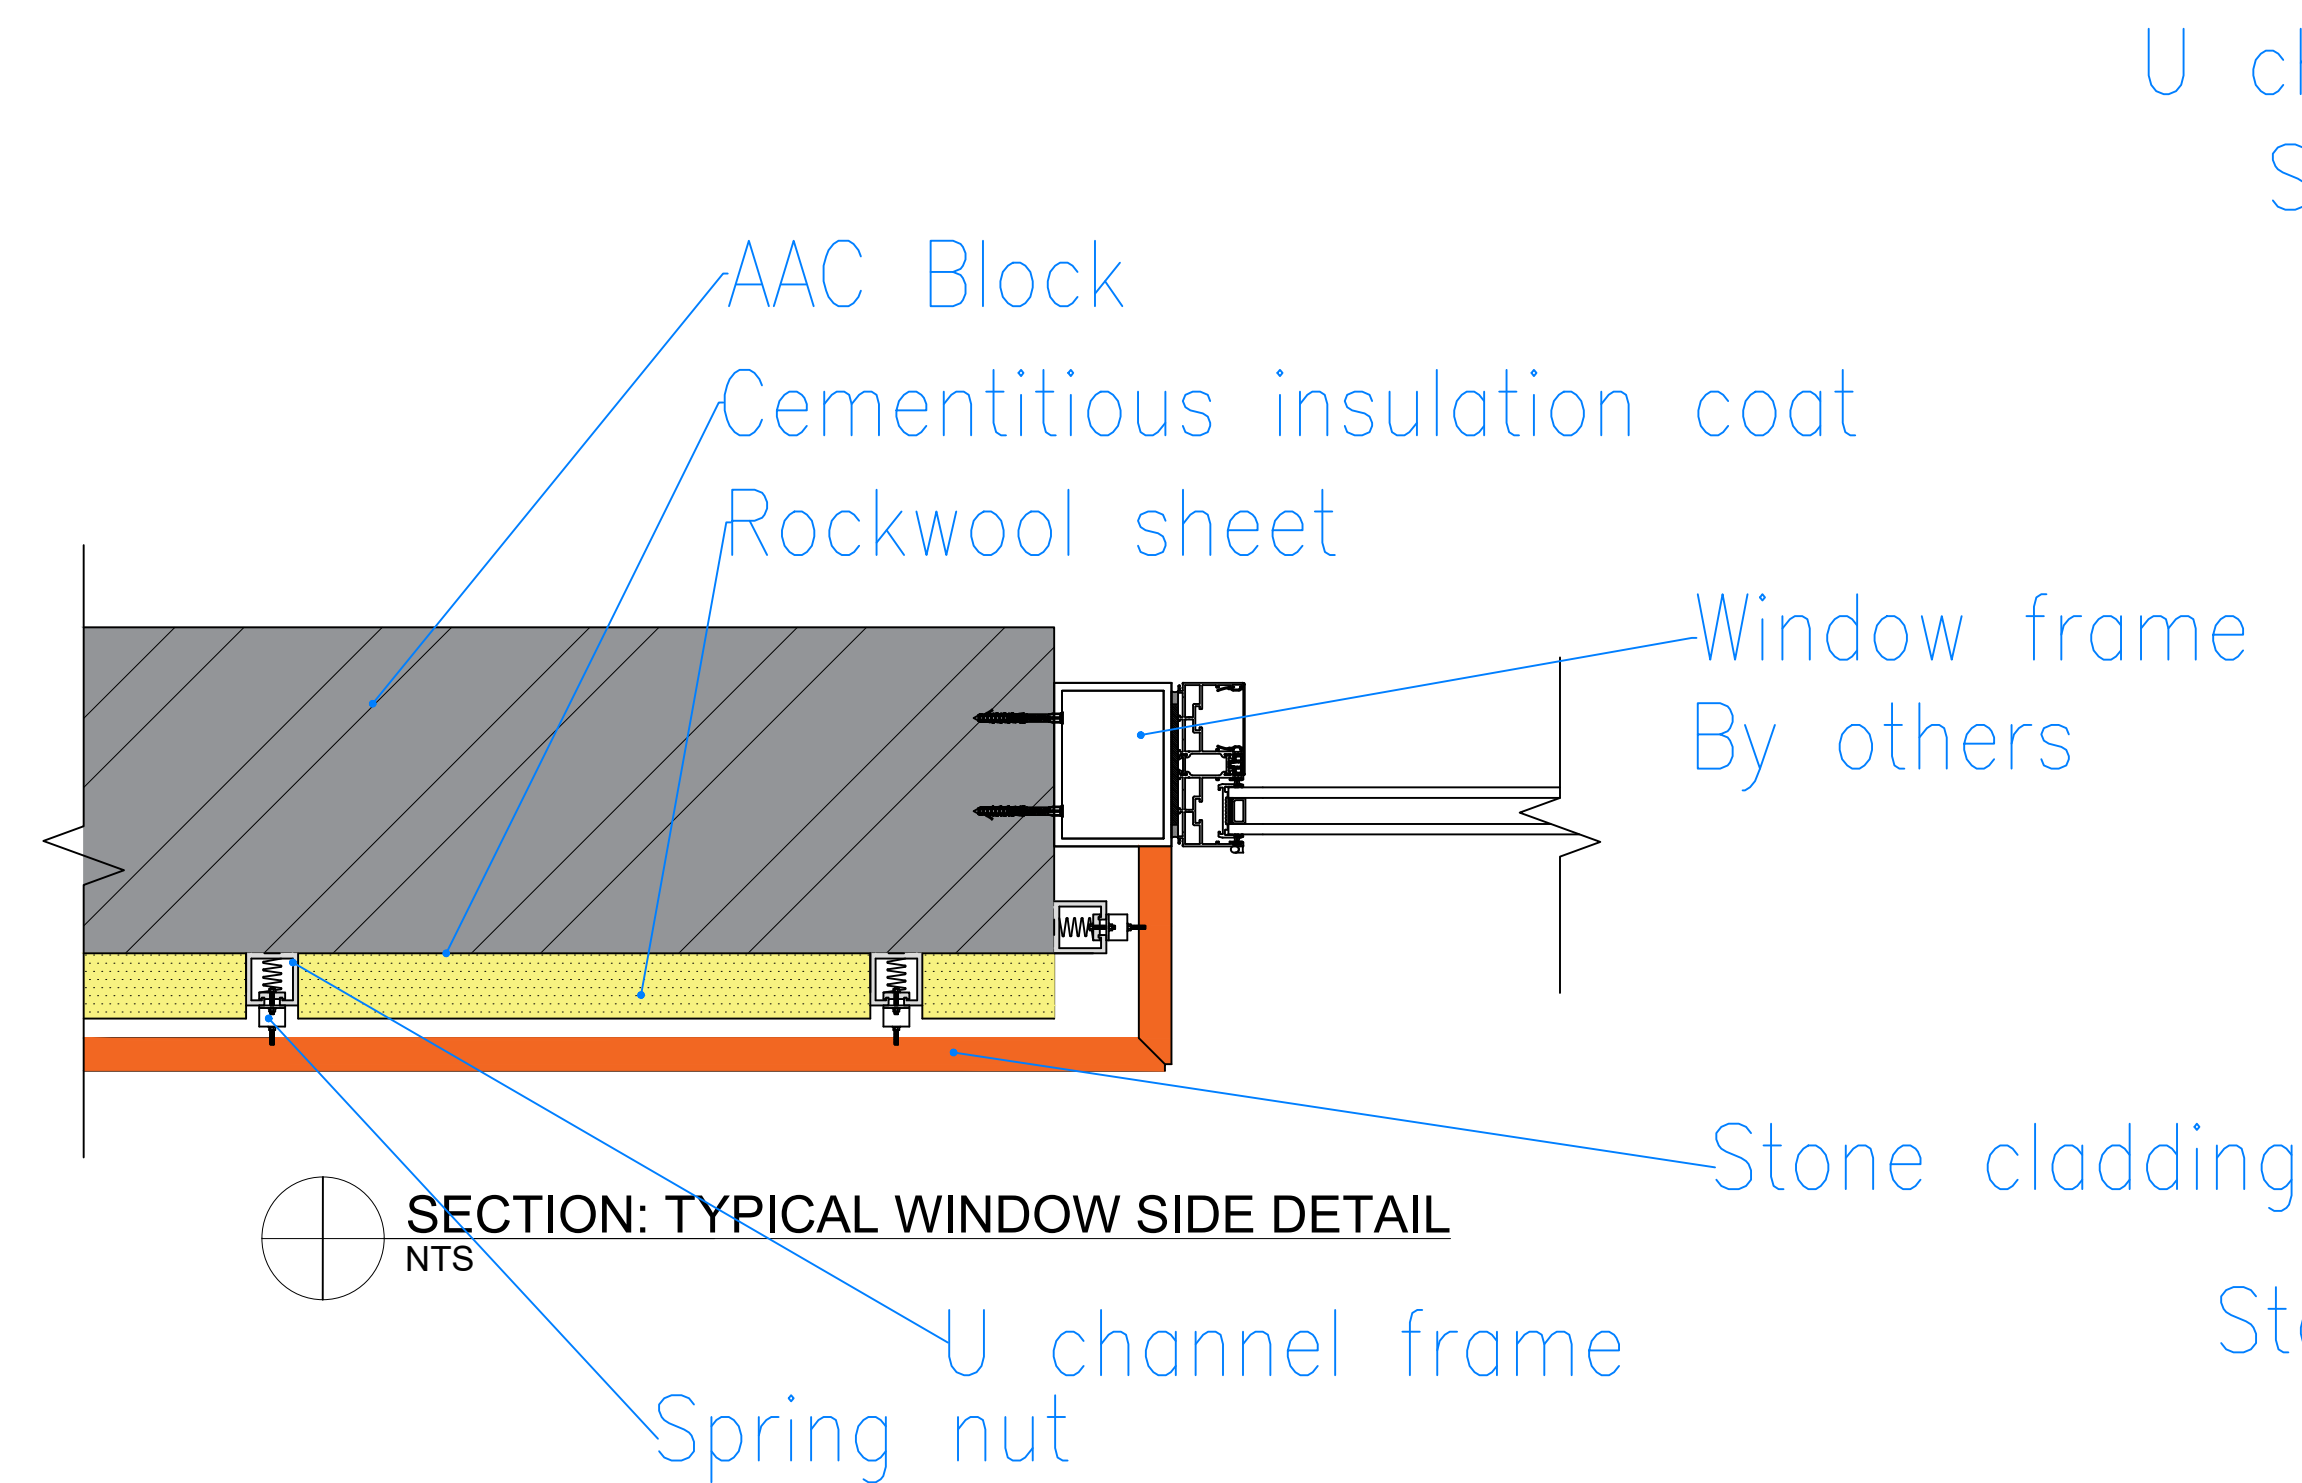

KEY PLAN

GENERAL NOTES

1. THIS DRAWING IS NOT TO BE SCALED. THE STATED DIMENSIONS ONLY ARE TO BE CONSIDERED.
2. FOR THE GENERAL NOTES & STANDARD DETAILS
3. ALL DIMENSIONS ARE IN MILLIMETERS AND LEVELS ARE IN METER UNLESS OTHERWISE NOTED.
4. SITE DIMENSION VERIFICATION REQUIRED PRIOR TO PRODUCTION.
5. ALL FINISHES AND IRONMONGERIES AS PER APPROVED MATERIAL SAMPLES ONLY.
6. ANY OBSERVED DISCREPANCY OF FINISHES AND DETAILS BETWEEN PROJECT DOCUMENTS (DRAWINGS, SPECIFICATION & BOQ), TO BE BROUGHT OUT TO DESIGNER FOR CONFIRMATION.

SHOP DRAWING/SUBMITTAL REVIEW

- ☐ STATUS A - APPROVED ☐ STATUS B - APPROVED WITH CHANGES / NOTES
- ☐ STATUS C - REVISED AND RESUBMIT ☐ STATUS D - REJECTED

SUBMITTAL WAS REVIEWED FOR DESIGN CONFORMITY, SPECIFICATION AND GENERAL CONFORMITY IN ACCORDANCE TO CONTRACT DOCUMENTS.

COMMENTS:

BY:..... DATE:.....

DRAWING REFERENCE

DWG. NO.	REV. NO.	DESCRIPTION

ISSUES

No.	Date	By	Revision Details

CLIENT

DAVID VON ROSEN VON HOEWEL

PROJECT

L117 - PALM JUMEIRAH

PLOT NO.: P/JRL117 LOCATION: PALM JUMEIRAH BLOCK: PALM JUMEIRAH

CONSULTANT:

ORIENT CROWN
ARCHITECTURAL

MAIN CONTRACTOR:
OLSEN & PARTNERS
INTERIORS

P.O. BOX: 283025, DUBAI U.A.E.
TEL: +971 4 5516500,
FAX: +971 4 5516501
email: info@opimena.com
www.opimena.com

DRAWING TITLE

External cladding pattern drawings
(Option 2 25mm stone thickness with 10mm Groove)

Drawn by Prepared by Checked by Approved by

File Ref. Date 26/10/2024 Scale AS SHOWN Revision 17

Drawing No.