


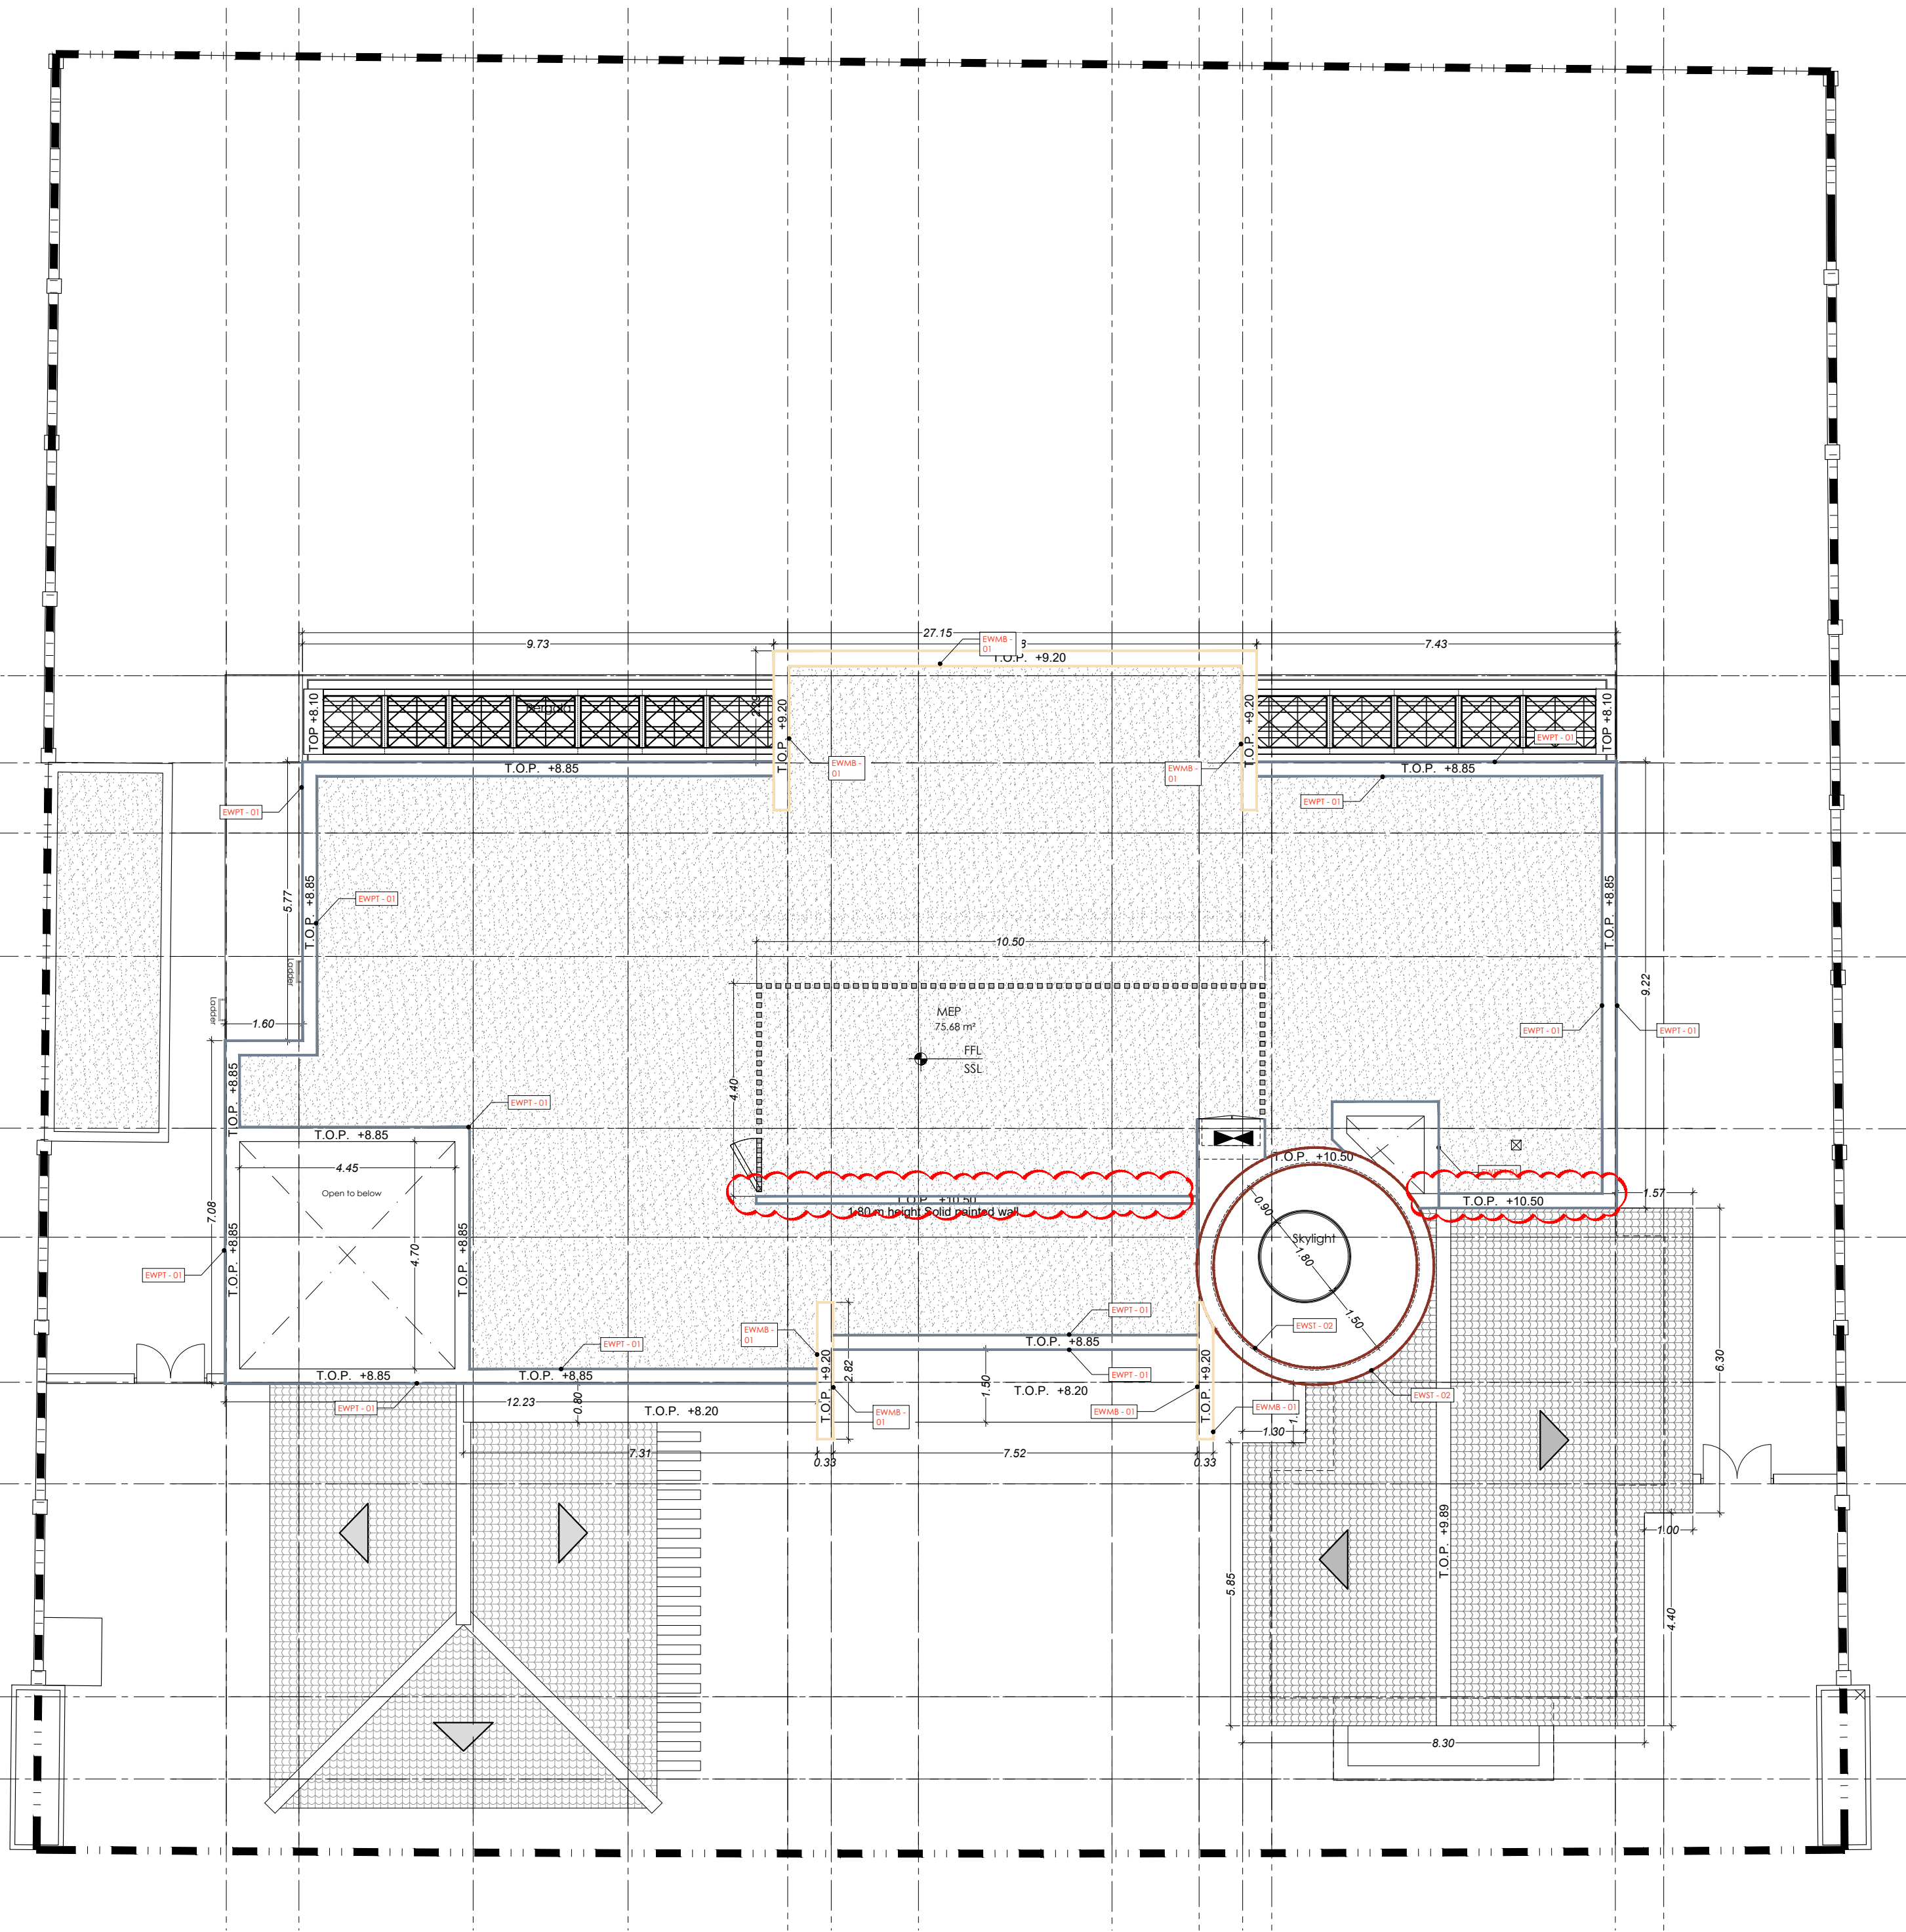

WALL FINISHING LAYOUT- ROOF FLOOR
Scale 1/100

LEGENDS

Code	Symbol	Description	Comments
EWAL - 01		ALUMINUM POWDER COATED, DARK GREY FINISH	
EWAL - 02		ALUMINUM POWDER-COATED WOOD IMITATION	
EWAL - 03		POWDER COATED ALUMINUM, WINDOWS, DARK GRAY FINISH	
ECLM - 01		HPL - HIGH PRESSURE LAMINATE SHEET - FLUTED WOOD IMITATION	
EWHL - 01		MAIN ENTRANCE DOOR STEEL CLADED WITH HPL WOOD IMITATION	
EWMB - 01		BEIGE TRAVERTINE ROMANO CLASSICO 2CM THK	
EWPR - 01		PITCHED ROOF TILE	
EWPT - 01		WHITE PAINT	
EWST - 01		GREY STONE-GREY ROUGH TEXTURE	
EWST - 02		FLAGSTONE CLADDING RANDOM CUT, ROUGH PIECES AND EDGES 20 TO 40MM THK (VARIABLE ROUGH STONE)	



1-THESE DRAWINGS ARE THE PROPERTY OF B8 ARCHITECTURE, P.O. BOX 390667, DUBAI. IT IS NOT ALLOWED TO REPRODUCE ITS CONTENTS IN ANY FORM OR USE THE INFORMATION CONTAINED THEREIN, EXCEPT FOR THE PURPOSE FOR WHICH IT IS INTENDED, AND WITH THE APPROVAL OF B8 ARCHITECTURE.

2-DIMENSIONS ARE IN METER UNLESS OTHERWISE STATED. ALL DIMENSIONS TO BE VERIFIED ON SITE AND APPROVED BY ENGINEER.

3-SHOP DRAWINGS OF MANUFACTURED ITEMS MUST BE APPROVED BY THE ARCHITECT ENGINEER BEFORE THE WORK IS STARTED ON THESE ITEMS.

4-THESE DRAWINGS SHOULD BE READ IN CONJUNCTION WITH OTHER RELEVANT ARCHITECTURAL, STRUCTURAL, MECHANICAL AND ELECTRICAL DRAWINGS AND ALL RELEVANT SECTIONS OF THE SPECIFICATIONS.

5-DON'T SCALE THE DRAWINGS. DRAWINGS ARE NOT NECESSARILY TO BE IN SCALE. VERIFY CONDITIONS AND DIMENSIONS AT THE JOB SITE PRIOR TO THE START OF CONSTRUCTION. IF DISCREPANCIES ARE FOUND, NOTIFY THE ARCHITECT FOR CLARIFICATION BEFORE COMMENCING THE WORK. EXPLICIT DIMENSIONS TAKE PRECEDENCE OVER SCALE.

NOTE :

Sellers' Disclaimer:
All measurements, dimensions, coordinates and drawings given in this floor plans, elevations, sections and details etc. (provided by the Purchaser) are to be in line with the Current Dubai Municipality drawing guidelines. Still the illustration, information and as such general guidance drawings may not be to exact scale. The Design reflected on these plans and other drawings are formulated from the Designs prepared and submitted by the Purchaser of the Property (or his Representative / Consultant / Contractor) prior to the commencement of works and therefore their accuracy in relation to actual construction cannot be confirmed by the Seller/Developer at such prior stage of construction. Further we make no guarantee, warranty or representation as to the accuracy and completeness of the above proposed design, in case of any variations or changes made by the Purchaser or their representative during the actual construction and development process, without notice. The proposed design and its construction works should commence only post securing applicable Authority Approvals / Permit by the Purchaser.

Drawing	Authorities	☐	Contractor	☒
00	To client	12.05.2026	IFC	
Rev.	Issued to	Date	Description	

Red clouds indicate the items changed from TD-02.
Green clouds indicate items currently under client approval.


NORTH DIRECTION:



PROJECT:

VILLA MODIFICATION

PLOT No: PJFRD139 AT PALM JUMEIRAH

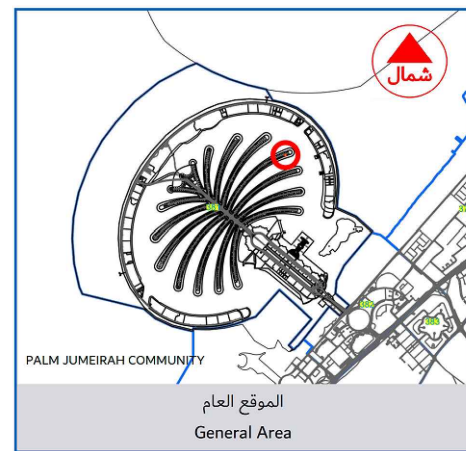

CLIENT:

Mrs. Jacqueline Tracey De Jager

MAIN CONSULTANT:



DESIGN ARCHITECT CONSULTANT:

B8 ARCHITECTURE



DRAWING DESCRIPTION:

ROOF FLOOR
EXTERNAL WALL FINISH
LAYOUT

SH.SIZE:	A1	SCALE:	1/100	PROJECT NO. P176
STAGE:	DRAWING N.	REV.		
ISSUE FOR CONSTRUCTION	B8-D139-IFC-AR-509	00		